
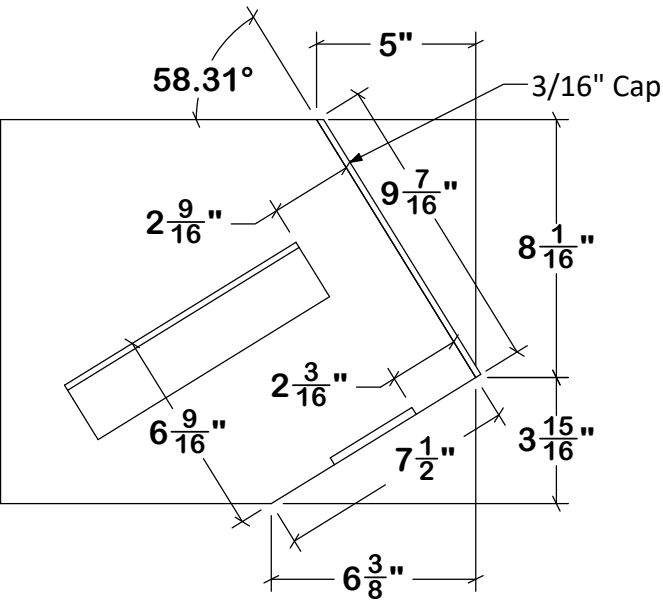
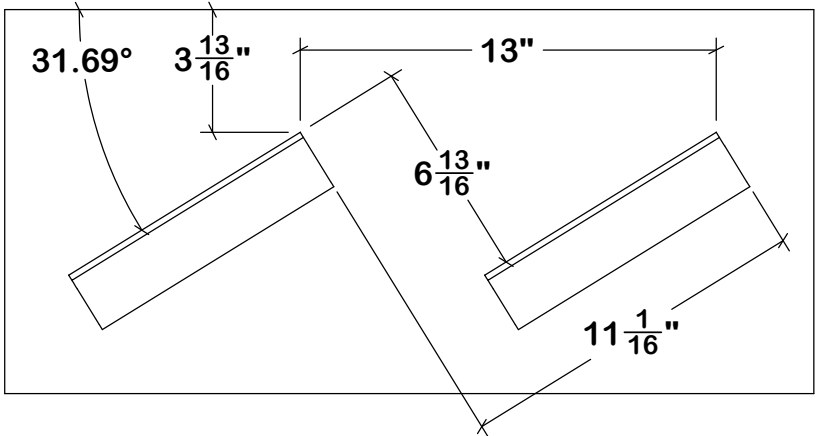
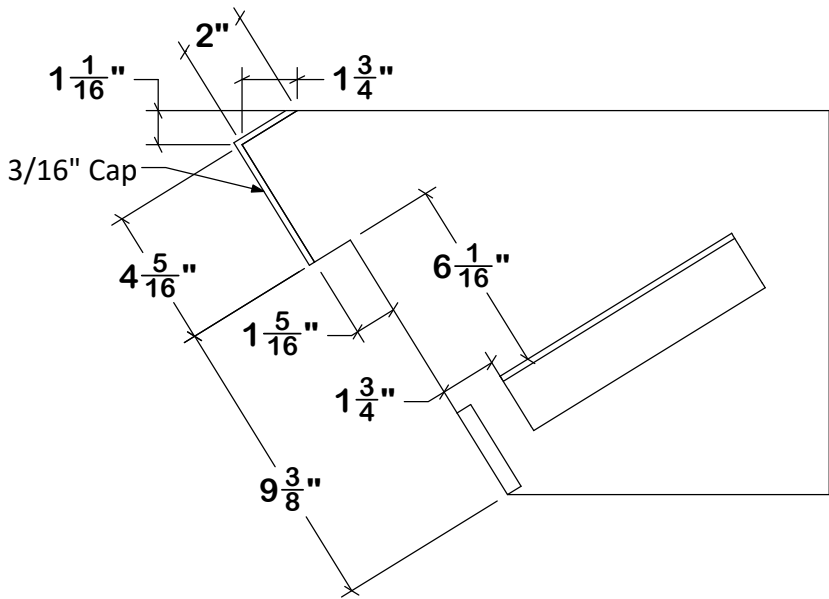


JOB START WORKSHEET									
Mile High Metal Works, Inc 7399 Miller Court, Frederick, CO 80504					303-485-8283 303-485-8206		Phone Fax		
Job #/ PO#:		590			674		Date:		6/8/2026
Job Name: CSI Construction - Flats at Sand Creek					Drafting				
Job Desc. Bld 3W Stair Core									
Paint:		Red Oxide Primed		Fabrication Completion Date:		0			
By		DCR		Install due date:		0		Install Hours 36.30	
Quantity	Total LF	Description			Quantity	Total LF	Description		
2	-	Stair Stringer 1 (674-S1R, 674-S1L)			-	-	-		
2	-	Stair Stringer 2 (674-S2R, 674-S2L)			-	-	-		
1	-	Stair Guardrail 1 (674-GR1)			-	-	-		
1	-	Stair Guardrail 2 (674-GR2)			-	-	-		
1	-	Landing Guardrail 1 (674-GR3)			-	-	-		
1	-	Landing Guardrail 2 (674-GR4)			-	-	-		
1	-	Stair Handrail 1 (674-HR1)			-	-	-		
1	-	Stair Handrail 2 (674-HR2)			-	-	-		
1	-	Stair Wallgrab 1 (674-WG1)			-	-	-		
1	-	Stair Wallgrab 2 (674-WG2)			-	-	-		
1	-	Cane Rail 1 (674-CR1)			-	-	-		
34	-	Large Riser Pan			-	-	-		
2	-	Small Riser Pan			-	-	-		
2	-	Nosing Angle			-	-	-		
2	-	Typ Pipe Sleeve			-	-	-		
-	-	-			-	-	-		
-	-	-			-	-	-		
-	-	-			Total Part Counts				
-	-	-				Quantity	Total LF		
-	-	-				53	0		
Project Manager		Quality Control	Quantity		Hardware			#pcs paint	
Danny Riddell		Checked by:	15		1/4" Tek Screws			15	
(720)522-0945			8		3/8"Ø x 3" Lag Screws			8	
			32		3/8"Ø x 5" Lag Screws			32	
Foreman		Checked by:	2		1/2"Ø x 4" Lag Screws			2	
0			2		1/2"Ø x 4" Wedge Anchors			2	
0			8		3/4"Ø x 8" A307 Thru Bolts W/ Nut And Washer			8	
		Checked by:	4		3/8"Ø x 3" Simpson Titen HD Anchors			4	
Job Contact 1			2		1/4"Ø x 3" Simpson SDS Screws			2	
0			36		43" x 12" Camp Logan Precast Treads			36	
0			144		3/8"Ø Fender Washers			144	
			144		3/8"Ø A563 Nuts			144	
Job Contact 2			8		Wall Handrail Brackets (Round)			8	
0			-		-			-	
0				Vendors					
NOTES:					By:	Date:	Notes:		
				Dencol					
				Metro					
				Platte Anchor					
				Drexel					
				Western Wire					
				Material					
				Job Site Address					
						0			

T:\590 Flats at Sand Creek (CO Springs)\Solidworks\Stairs\Bld 3W Stair Core FAB

All Dims Before End Caps

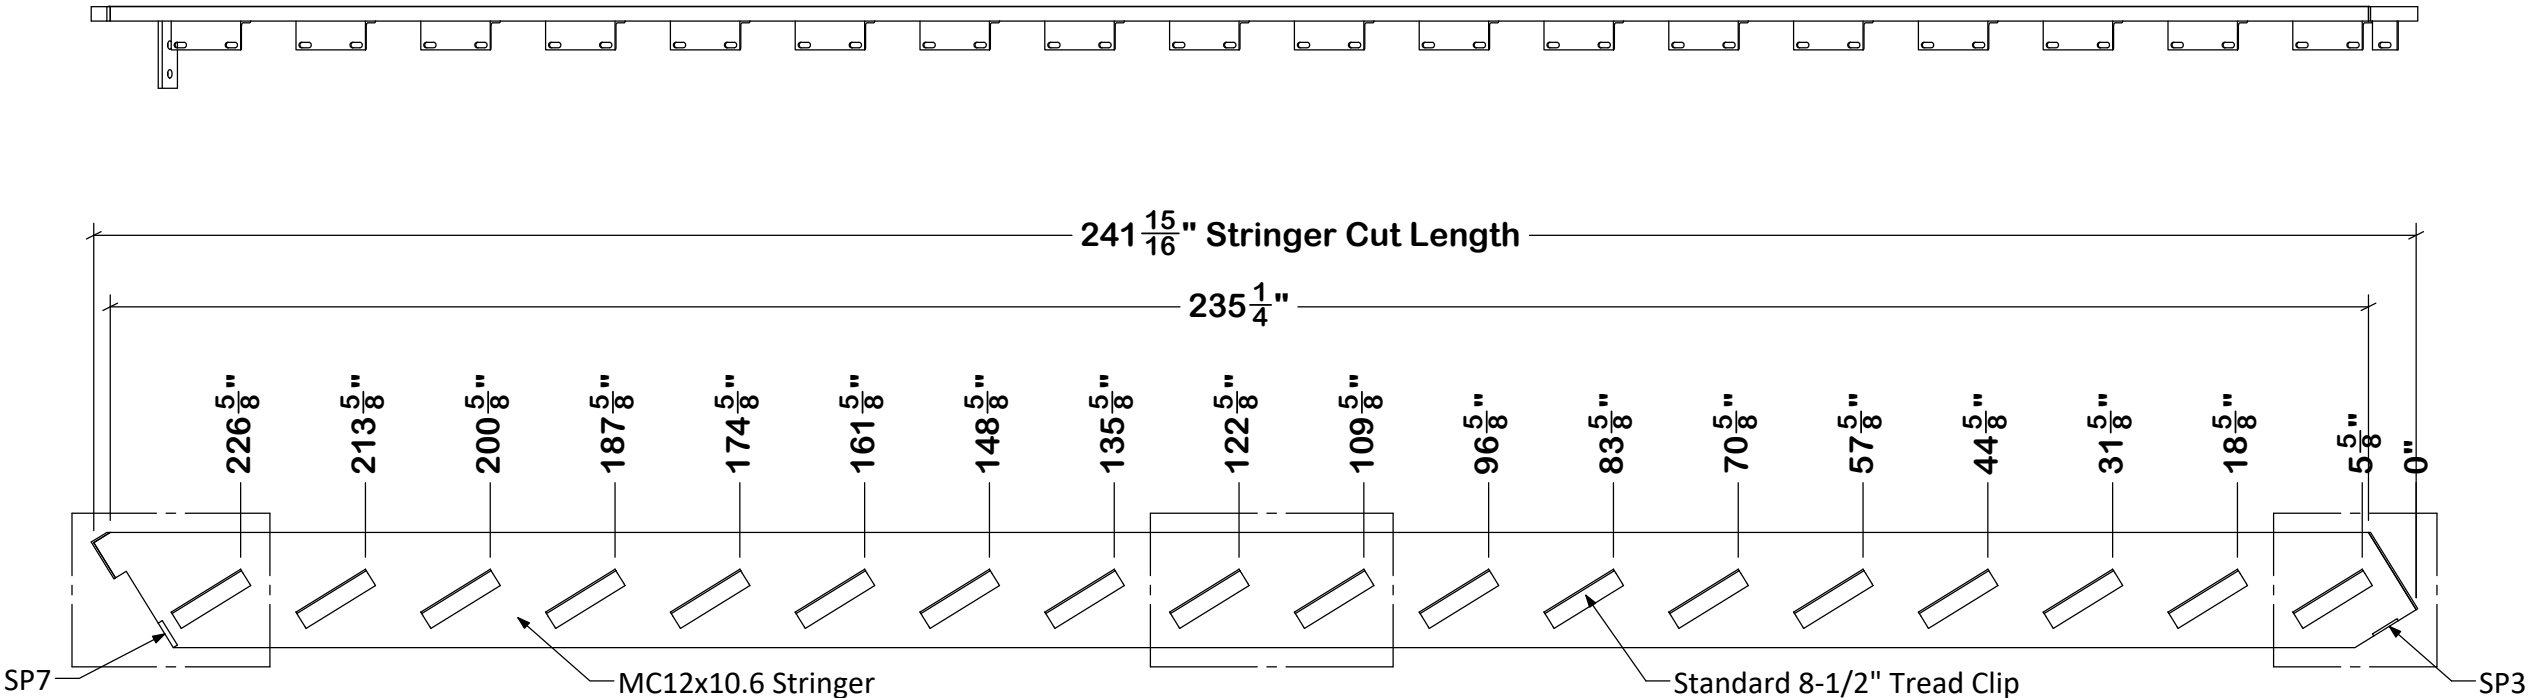

Stair Stringer 1 "674-S1R"- QTY (1) As Shown
"674-S1L"- QTY (1) Mirrored

Index	Date	Description	By



Mile High Metal Works, Inc.
7399 Miller Court, Unit A, Frederick, CO 80504
Office 303-485-8283 Fax 303-485-8206

Project Name:
CSI Construction - Flats At
Sand Creek

Description:
Bld 3W Stair Core

Date:
6/5/2026

Job #:
590-674





Color:
Red Oxide
Primed

By:
DCR

Rev:
0

Drawing:
F1

All Dims Before End Caps

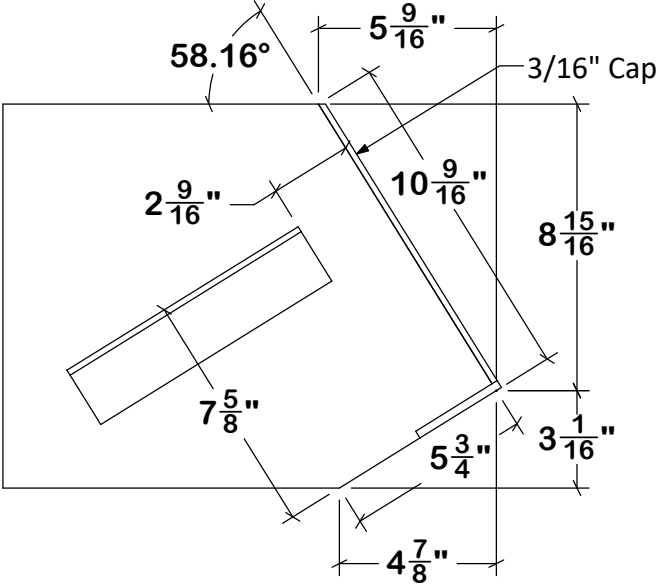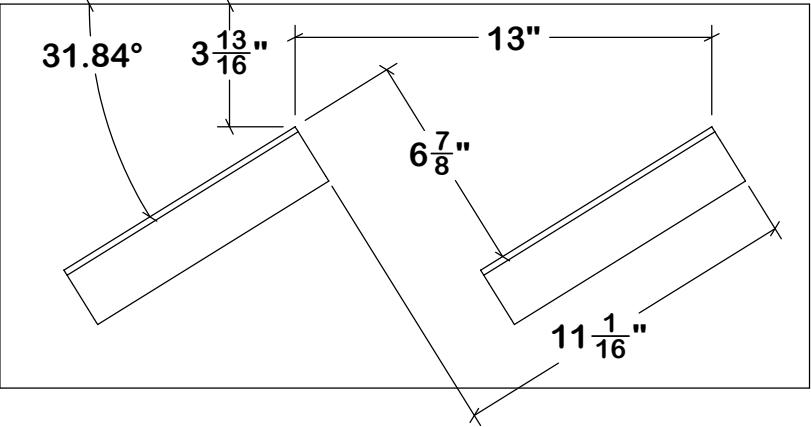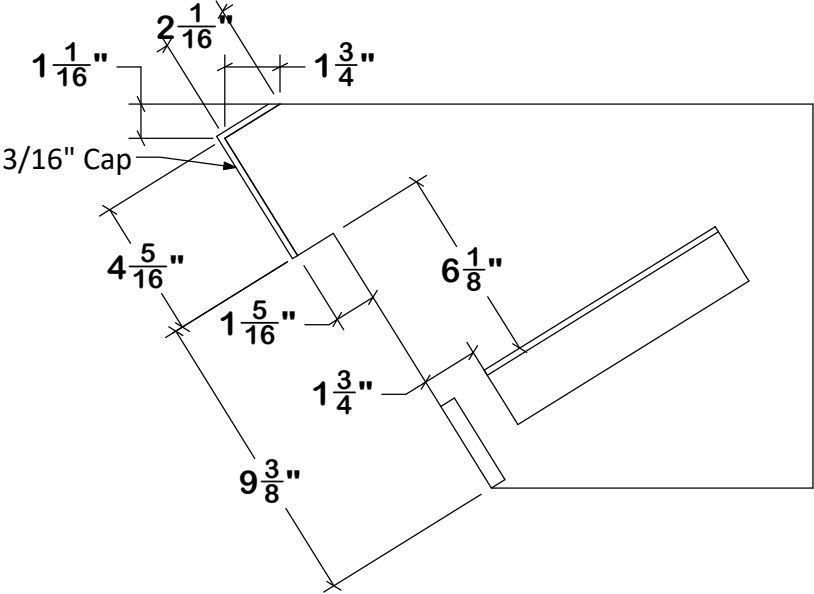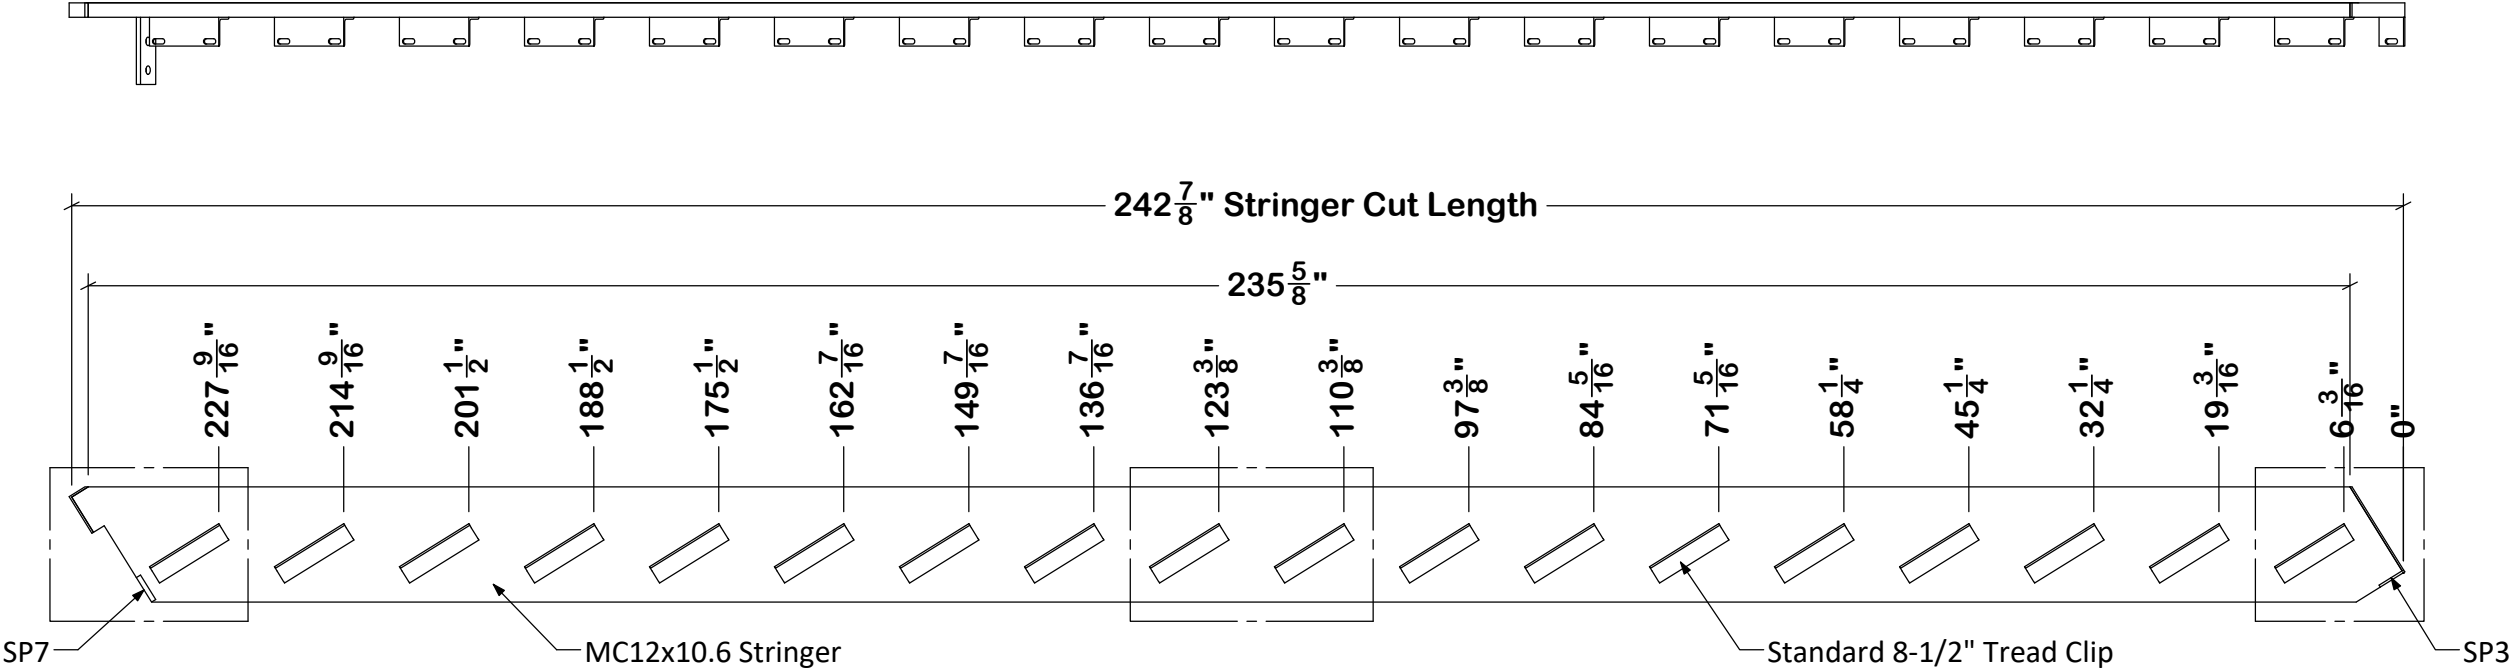

Stair Stringer 1 "674-S2R"- QTY (1) As Shown
"674-S2L"- QTY (1) Mirrored

T:\590 Flats at Sand Creek (CO Springs)\Solidworks\Stairs\Bld 3W Stair Core FAB

Index	Date	Description	By



Mile High Metal Works, Inc.
7399 Miller Court, Unit A, Frederick, CO 80504
Office 303-485-8283 Fax 303-485-8206

Project Name:
CSI Construction - Flats At
Sand Creek

Description:
Bld 3W Stair Core

Date:
6/5/2026

Job #:
590-674


Color:
Red Oxide
Primed

By:
DCR

Rev:
0

Drawing:
F2


T:\590 Flats at Sand Creek (CO Springs)\Solidworks\Stairs\Bld 3W Stair Core FAB

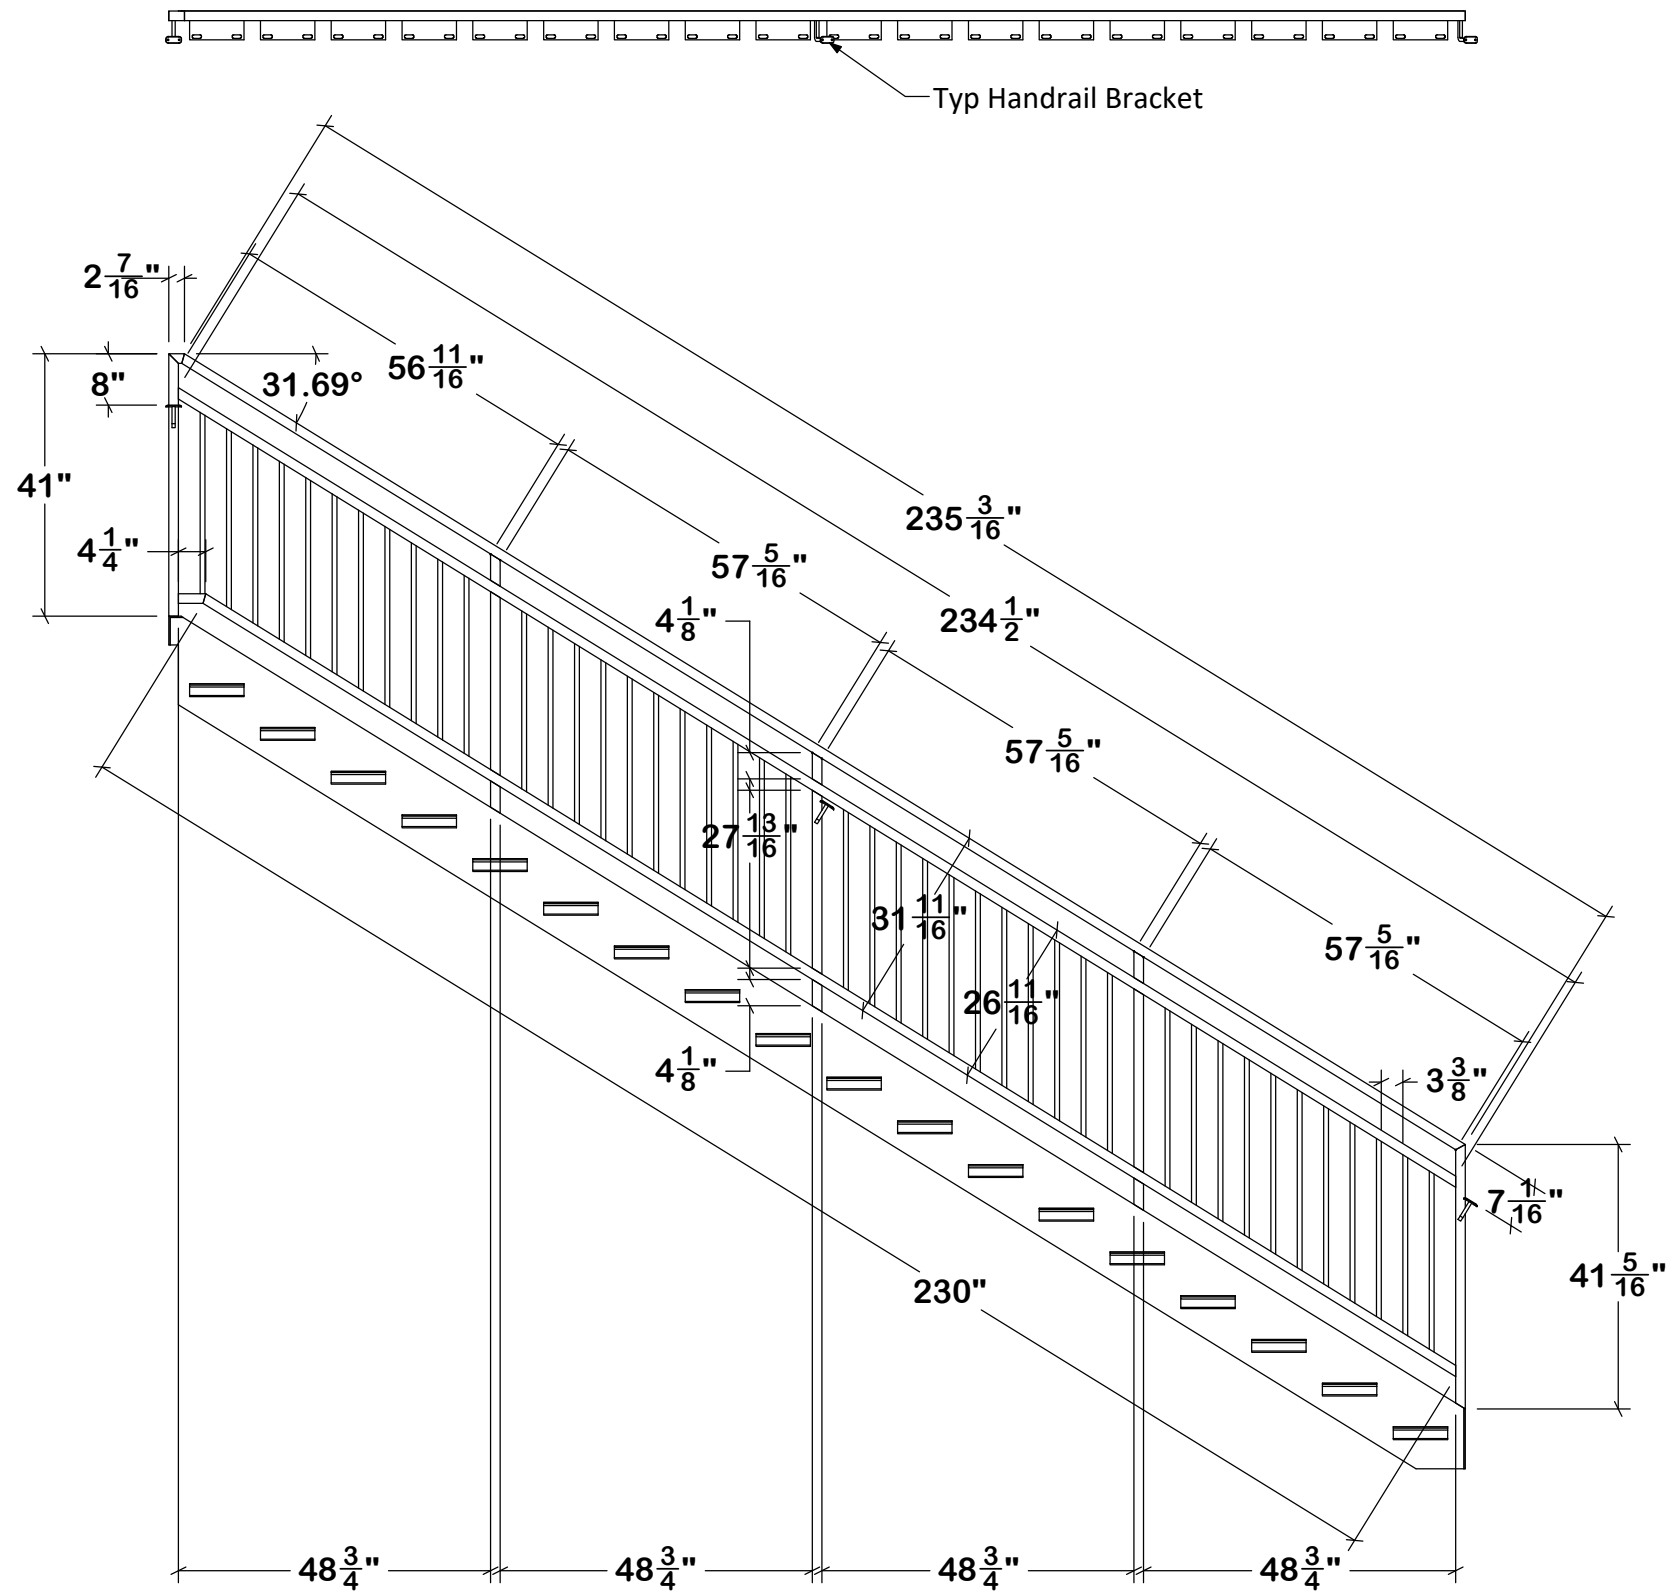

MATERIALS

1-1/2" Sq 11 Ga. TS Frame

3/4" Sq. 16 Ga. TS Pickets

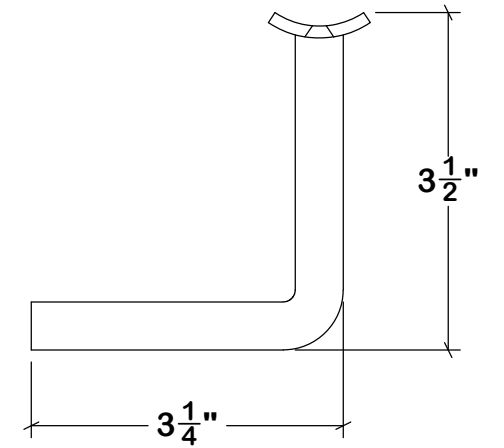

Typ Handrail Bracket

Stair Guardrail 1 "674-GR1"- QTY (1)

Index	Date	Description	By


Mile High Metal Works, Inc.
7399 Miller Court, Unit A, Frederick, CO 80504
Office 303-485-8283 Fax 303-485-8206

Project Name:
CSI Construction - Flats At
Sand Creek

Description:
Bld 3W Stair Core

Date:
6/5/2026

Job #:
590-674


Color:
Red Oxide
Primed

By:
DCR

Rev:
0

Drawing:
F3


T:\590 Flats at Sand Creek (CO Springs)\Solidworks\Stairs\Bld 3W Stair Core FAB

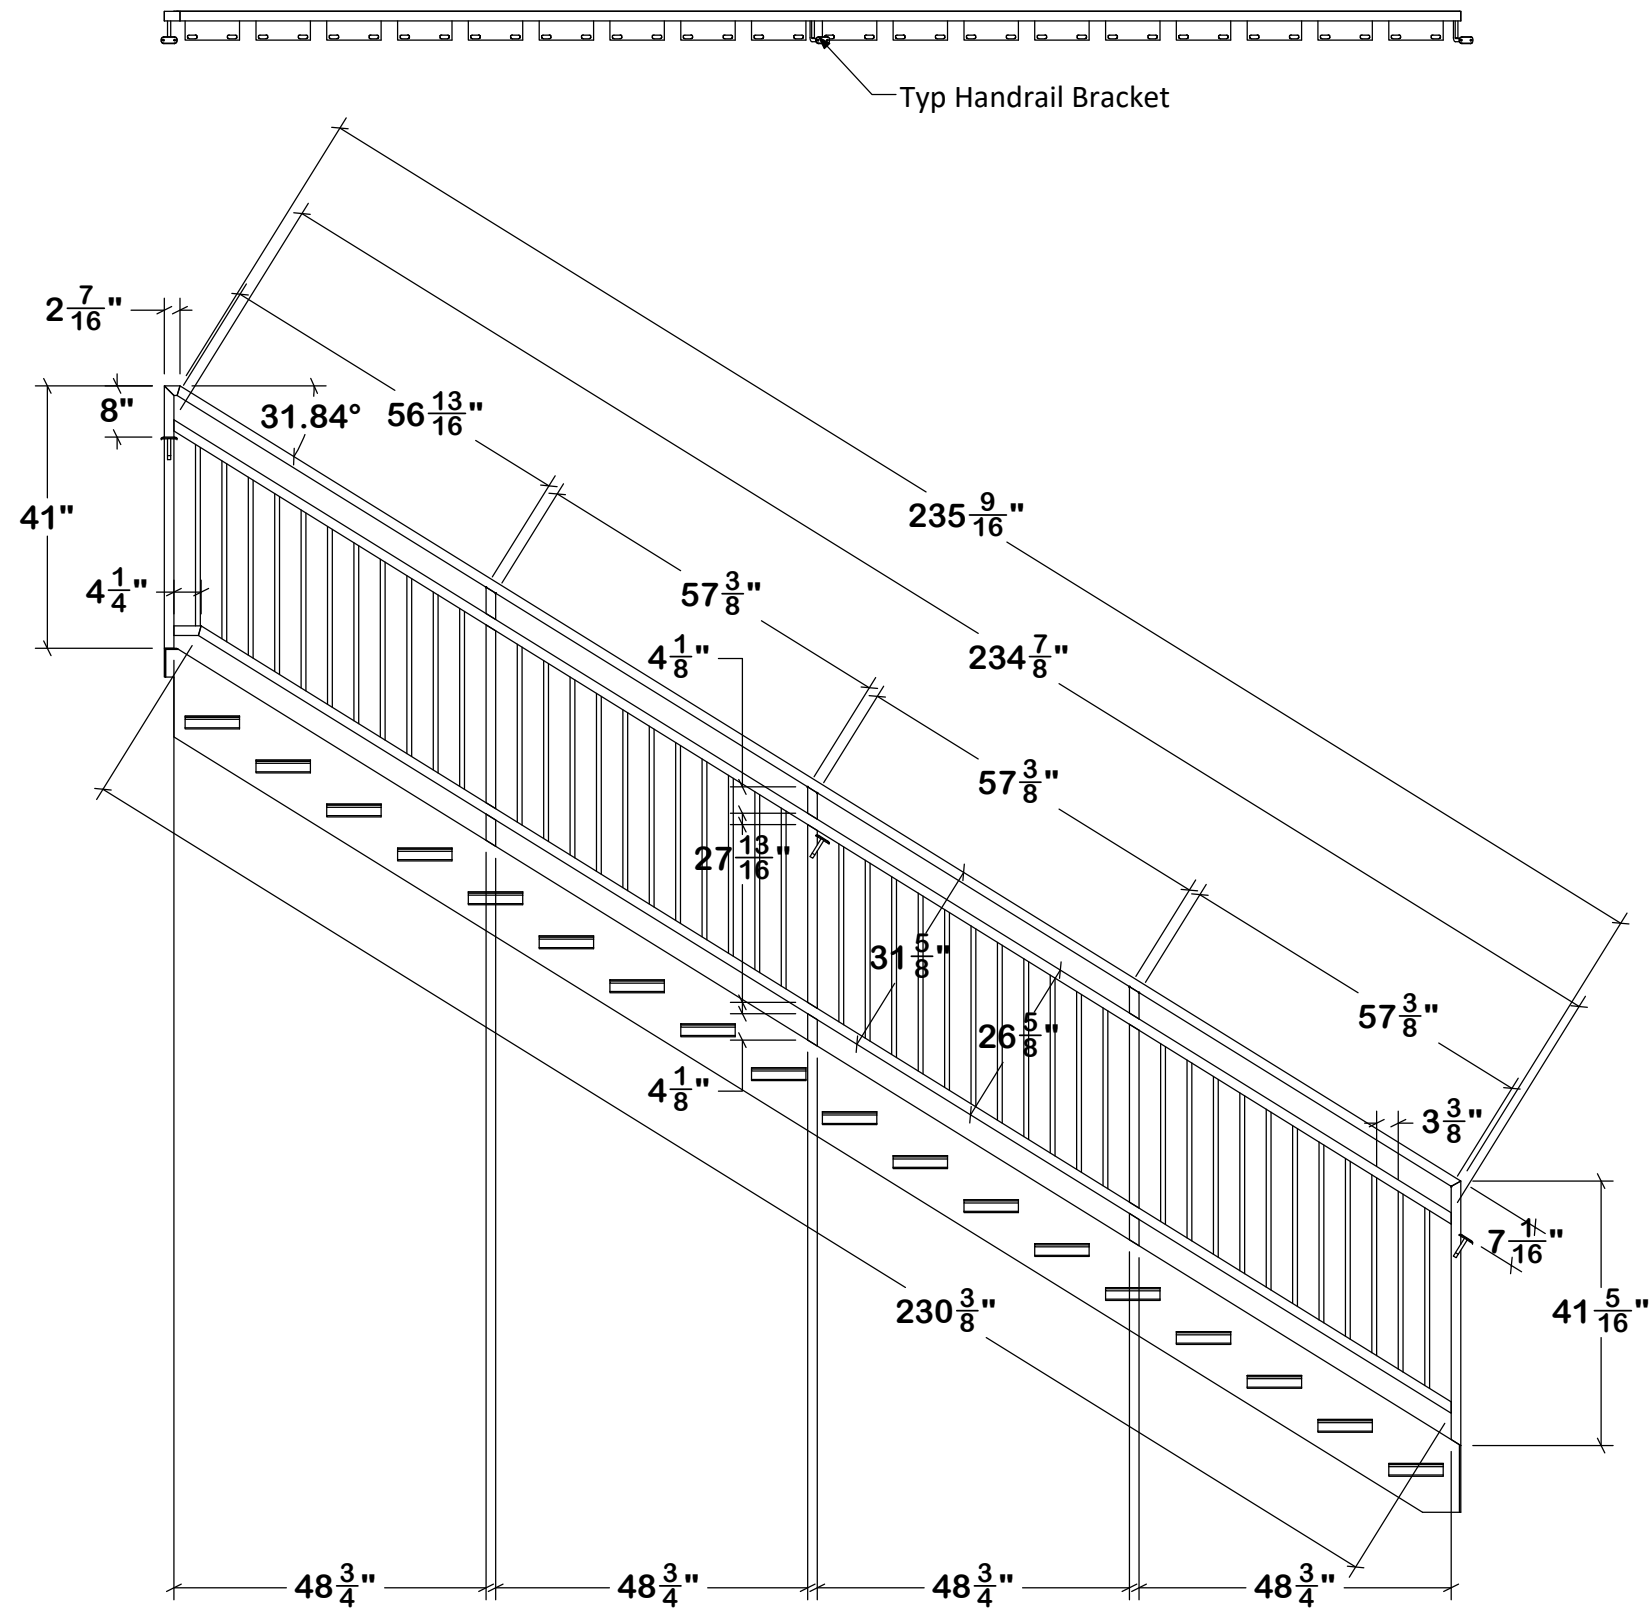

MATERIALS

1-1/2" Sq 11 Ga. TS Frame

3/4" Sq. 16 Ga. TS Pickets

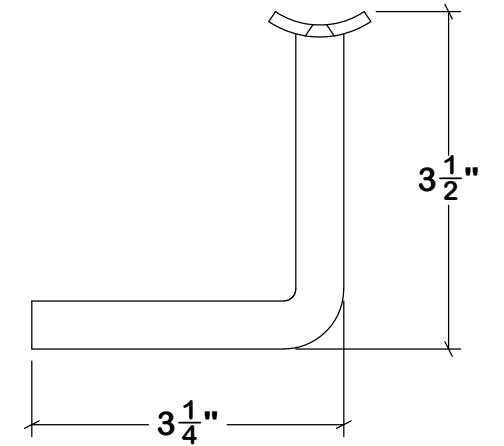

Typ Handrail Bracket

Stair Guardrail 2 "674-GR2"- QTY (1)

Index	Date	Description	By


Mile High Metal Works, Inc.
7399 Miller Court, Unit A, Frederick, CO 80504
Office 303-485-8283 Fax 303-485-8206

Project Name:
CSI Construction - Flats At
Sand Creek

Description:
Bld 3W Stair Core

Date:
6/5/2026

Job #:
590-674



Color:
Red Oxide
Primed

By:
DCR

Rev:
0

Drawing:
F4


T:\590 Flats at Sand Creek (CO Springs)\Solidworks\Stairs\Bld 3W Stair Core FAB

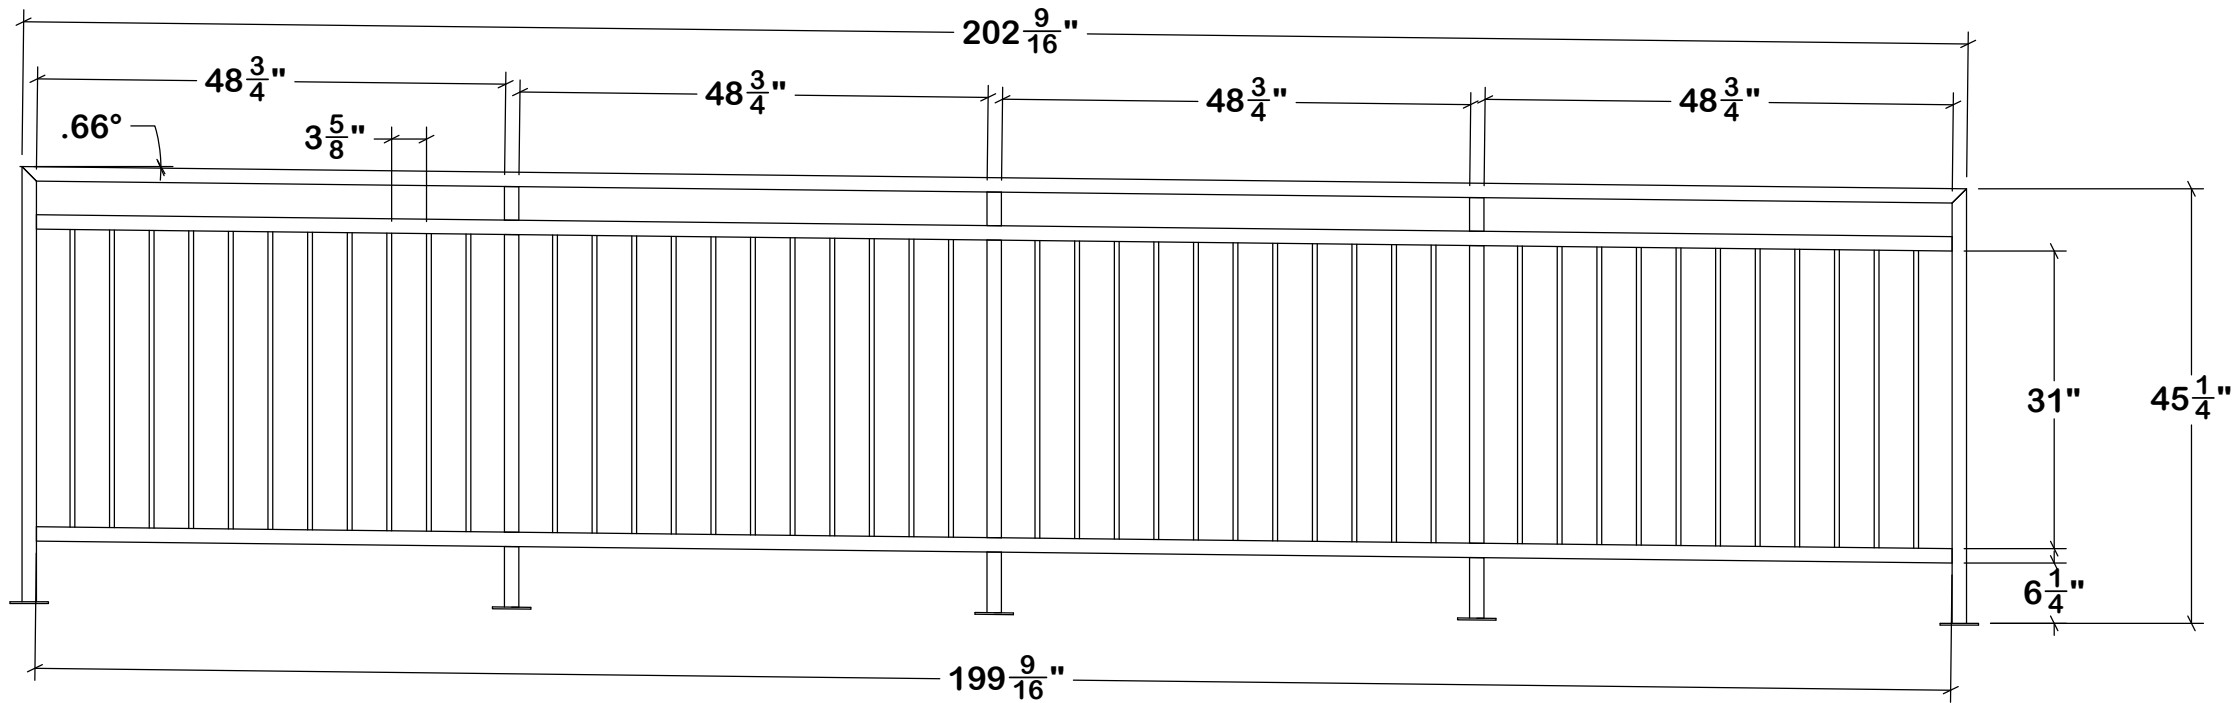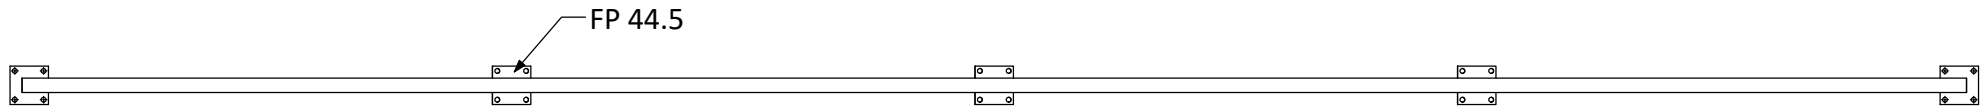

MATERIALS

1-1/2" Sq 11 Ga. TS Frame

3/4" Sq. 16 Ga. TS Pickets

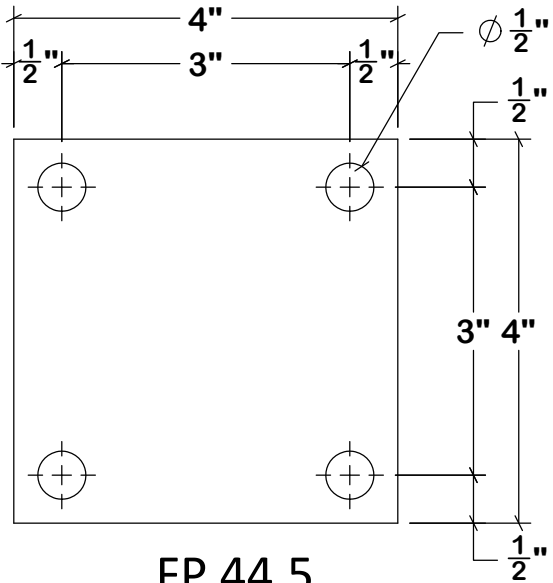

Landing Guardrail 1 "674-GR3"- QTY (1)

Index	Date	Description	By



Mile High Metal Works, Inc.
7399 Miller Court, Unit A, Frederick, CO 80504
Office 303-485-8283 Fax 303-485-8206

Project Name:

CSI Construction - Flats At Sand Creek

Description:

Bld 3W Stair Core

Date:

6/5/2026

Job #:

590-674

Color:

Red Oxide Primed

By:

DCR



Rev:

0

Drawing:

F5

T:\590 Flats at Sand Creek (CO Springs)\Solidworks\Stairs\Bld 3W Stair Core FAB

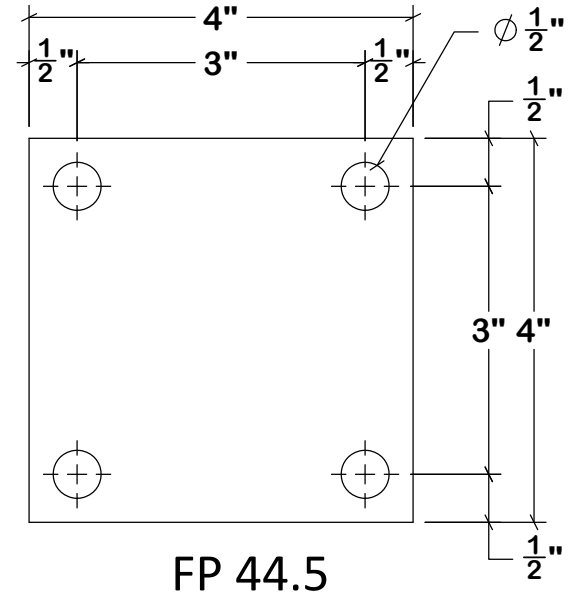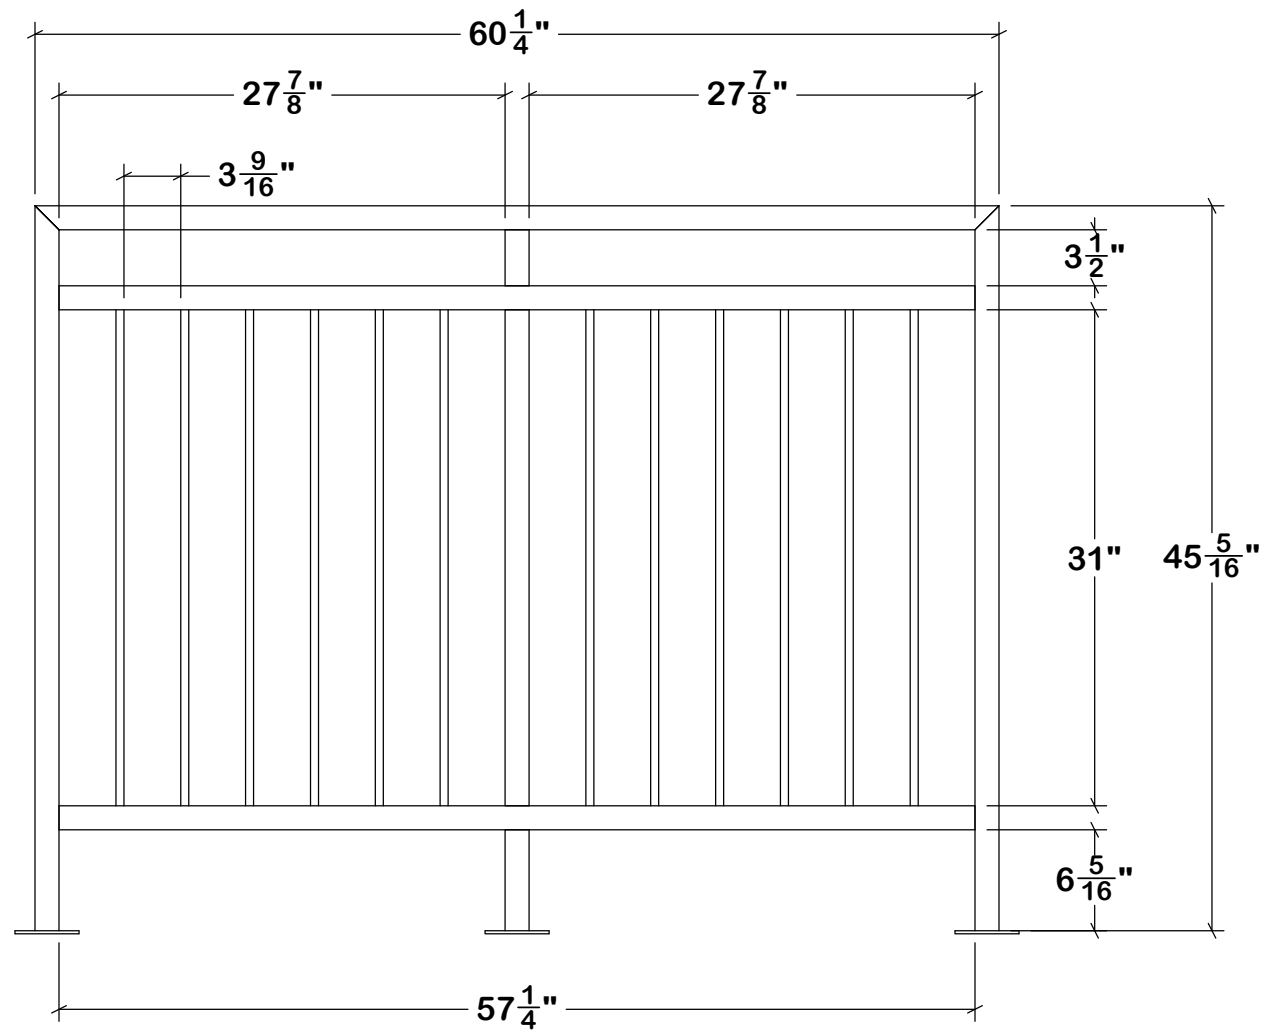

MATERIALS

1-1/2" Sq 11 Ga. TS Frame

3/4" Sq. 16 Ga. TS Pickets

Landing Guardrail 2 "674-GR4"- QTY (1)

Index	Date	Description	By



Mile High Metal Works, Inc.
7399 Miller Court, Unit A, Frederick, CO 80504
Office 303-485-8283 Fax 303-485-8206

Project Name:
CSI Construction - Flats At
Sand Creek

Description:
Bld 3W Stair Core

Date:
6/5/2026

Job #:
590-674



Color:
Red Oxide
Primed

By:
DCR

Rev:
0

Drawing:
F6

T:\590 Flats at Sand Creek (CO Springs)\Solidworks\Stairs\Bld 3W Stair Core FAB

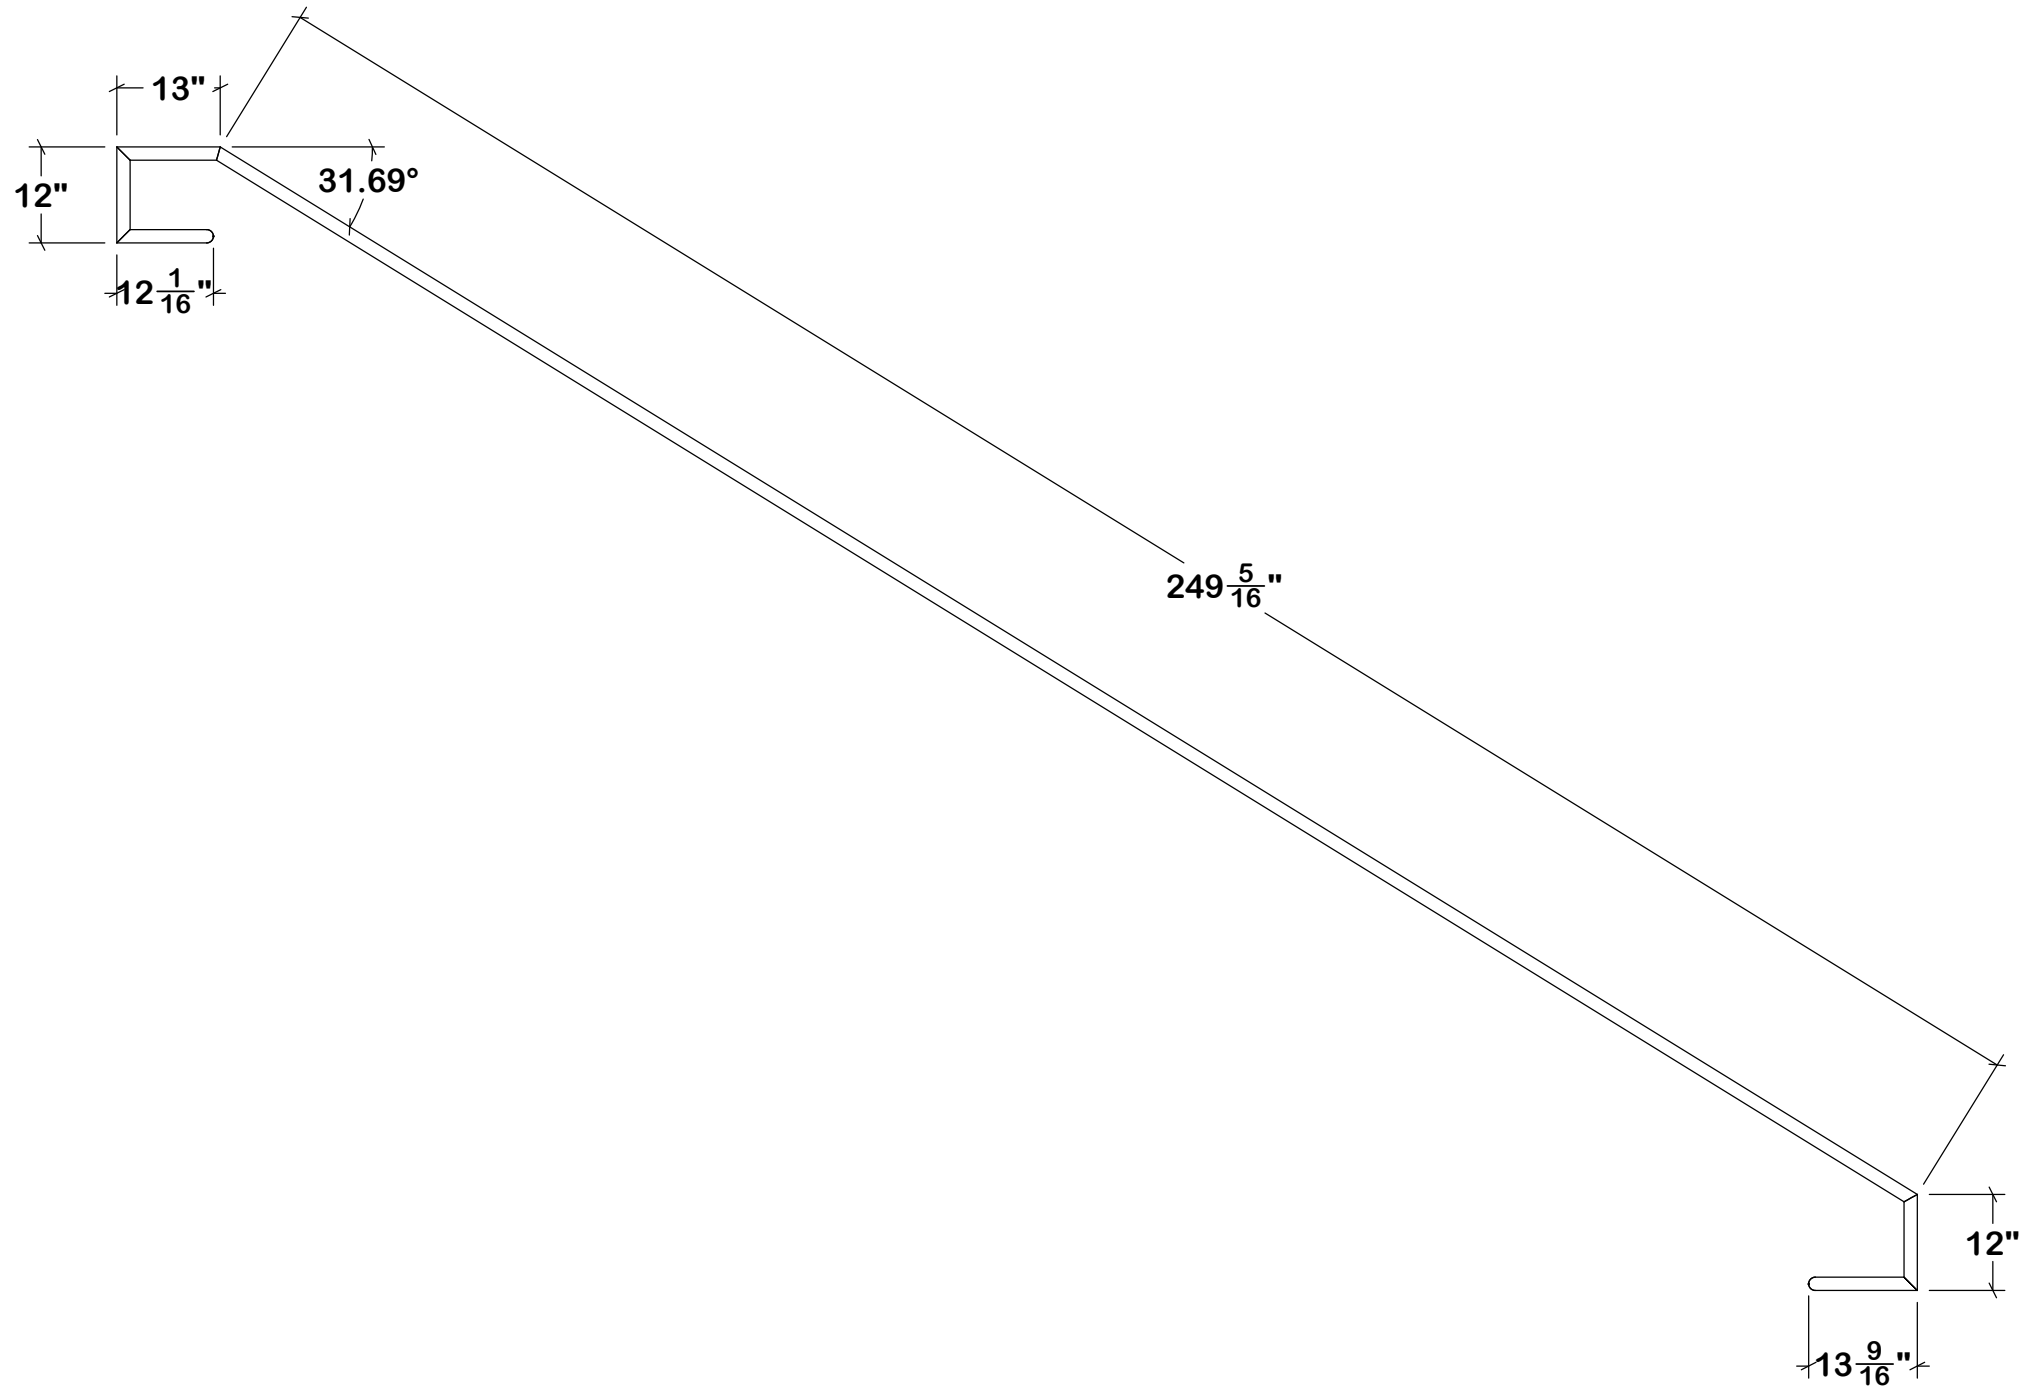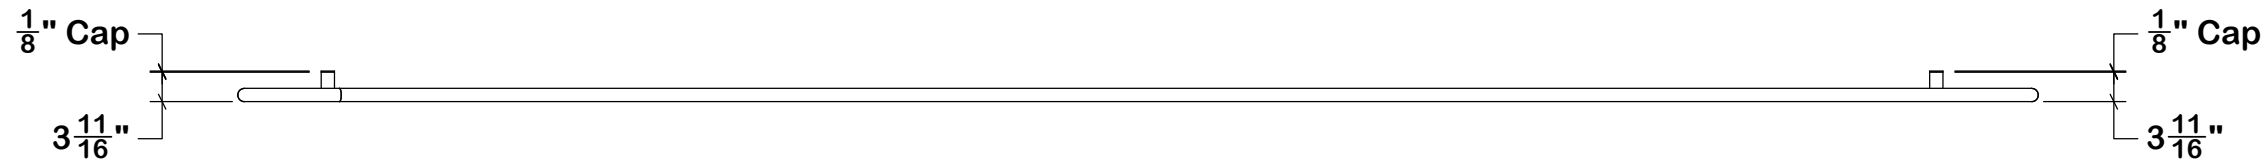

MATERIALS

1-1/4" SCH 10 Pipe

Stair Handrail 1 "674-HR1"- QTY (1)

Index	Date	Description	By



Mile High Metal Works, Inc.
7399 Miller Court, Unit A, Frederick, CO 80504
Office 303-485-8283 Fax 303-485-8206

Project Name:
CSI Construction - Flats At
Sand Creek

Description:
Bld 3W Stair Core

Date:
6/5/2026

Job #:
590-674

Color:
Red Oxide
Primed

By:
DCR

Rev:
0


Drawing:
F7

T:\590 Flats at Sand Creek (CO Springs)\Solidworks\Stairs\Bld 3W Stair Core FAB



MATERIALS

1-1/4" SCH 10 Pipe

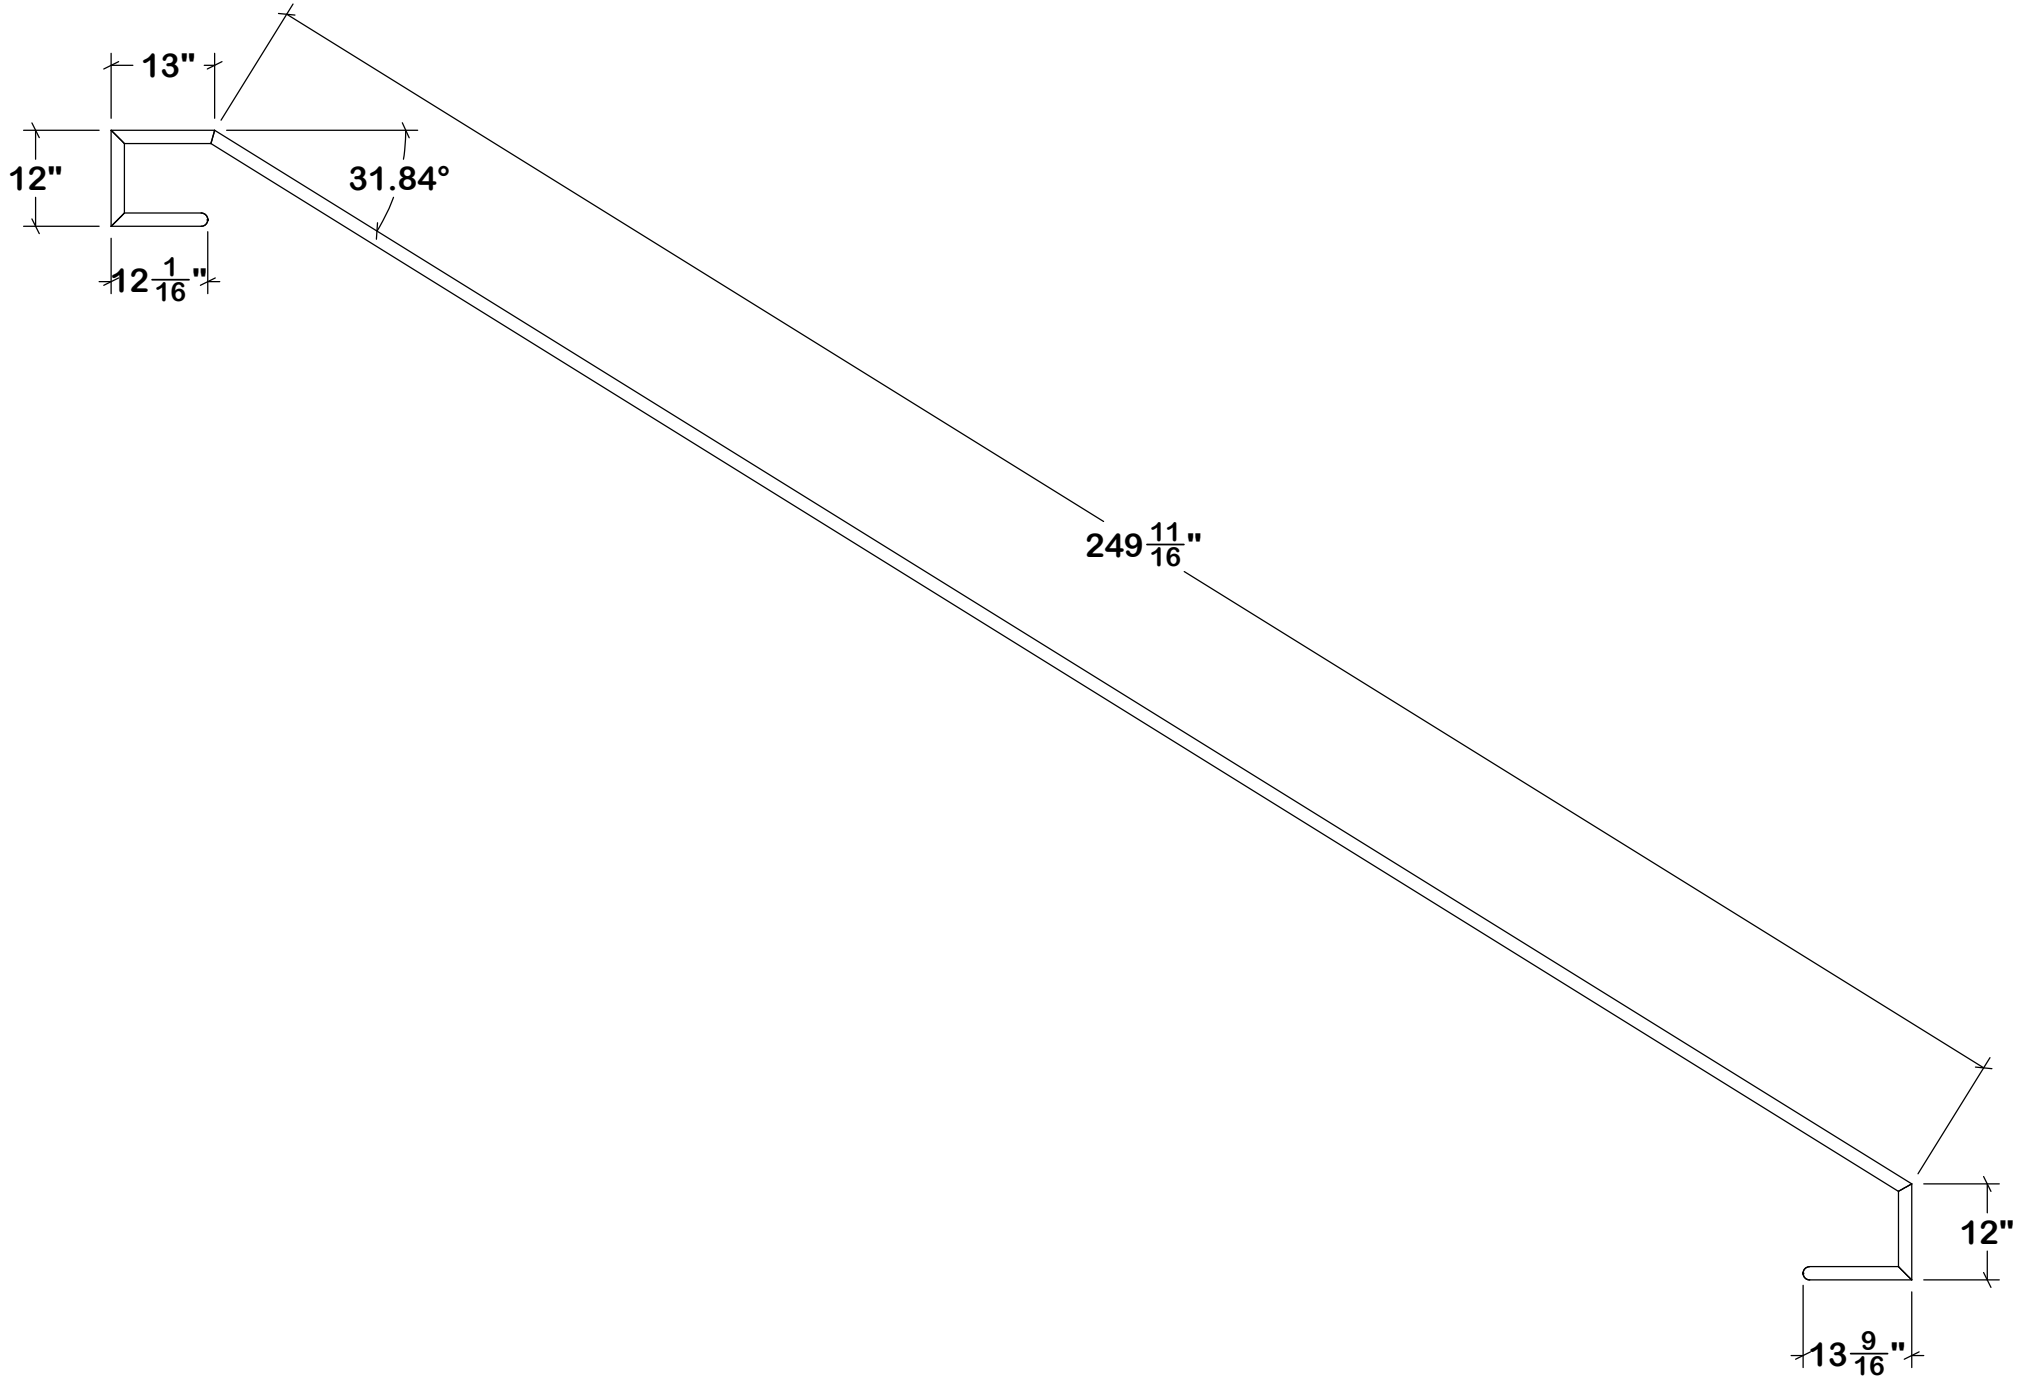

Stair Handrail 2 "674-HR2"- QTY (1)

Index	Date	Description	By



Mile High Metal Works, Inc.
7399 Miller Court, Unit A, Frederick, CO 80504
Office 303-485-8283 Fax 303-485-8206

Project Name:
CSI Construction - Flats At
Sand Creek

Description:
Bld 3W Stair Core

Date:
6/5/2026

Job #:
590-674

Color:
Red Oxide
Primed

By:
DCR

Rev:
0


Drawing:
F8

T:\590 Flats at Sand Creek (CO Springs)\Solidworks\Stairs\Bld 3W Stair Core FAB



MATERIALS

1-1/4" SCH 10 Pipe

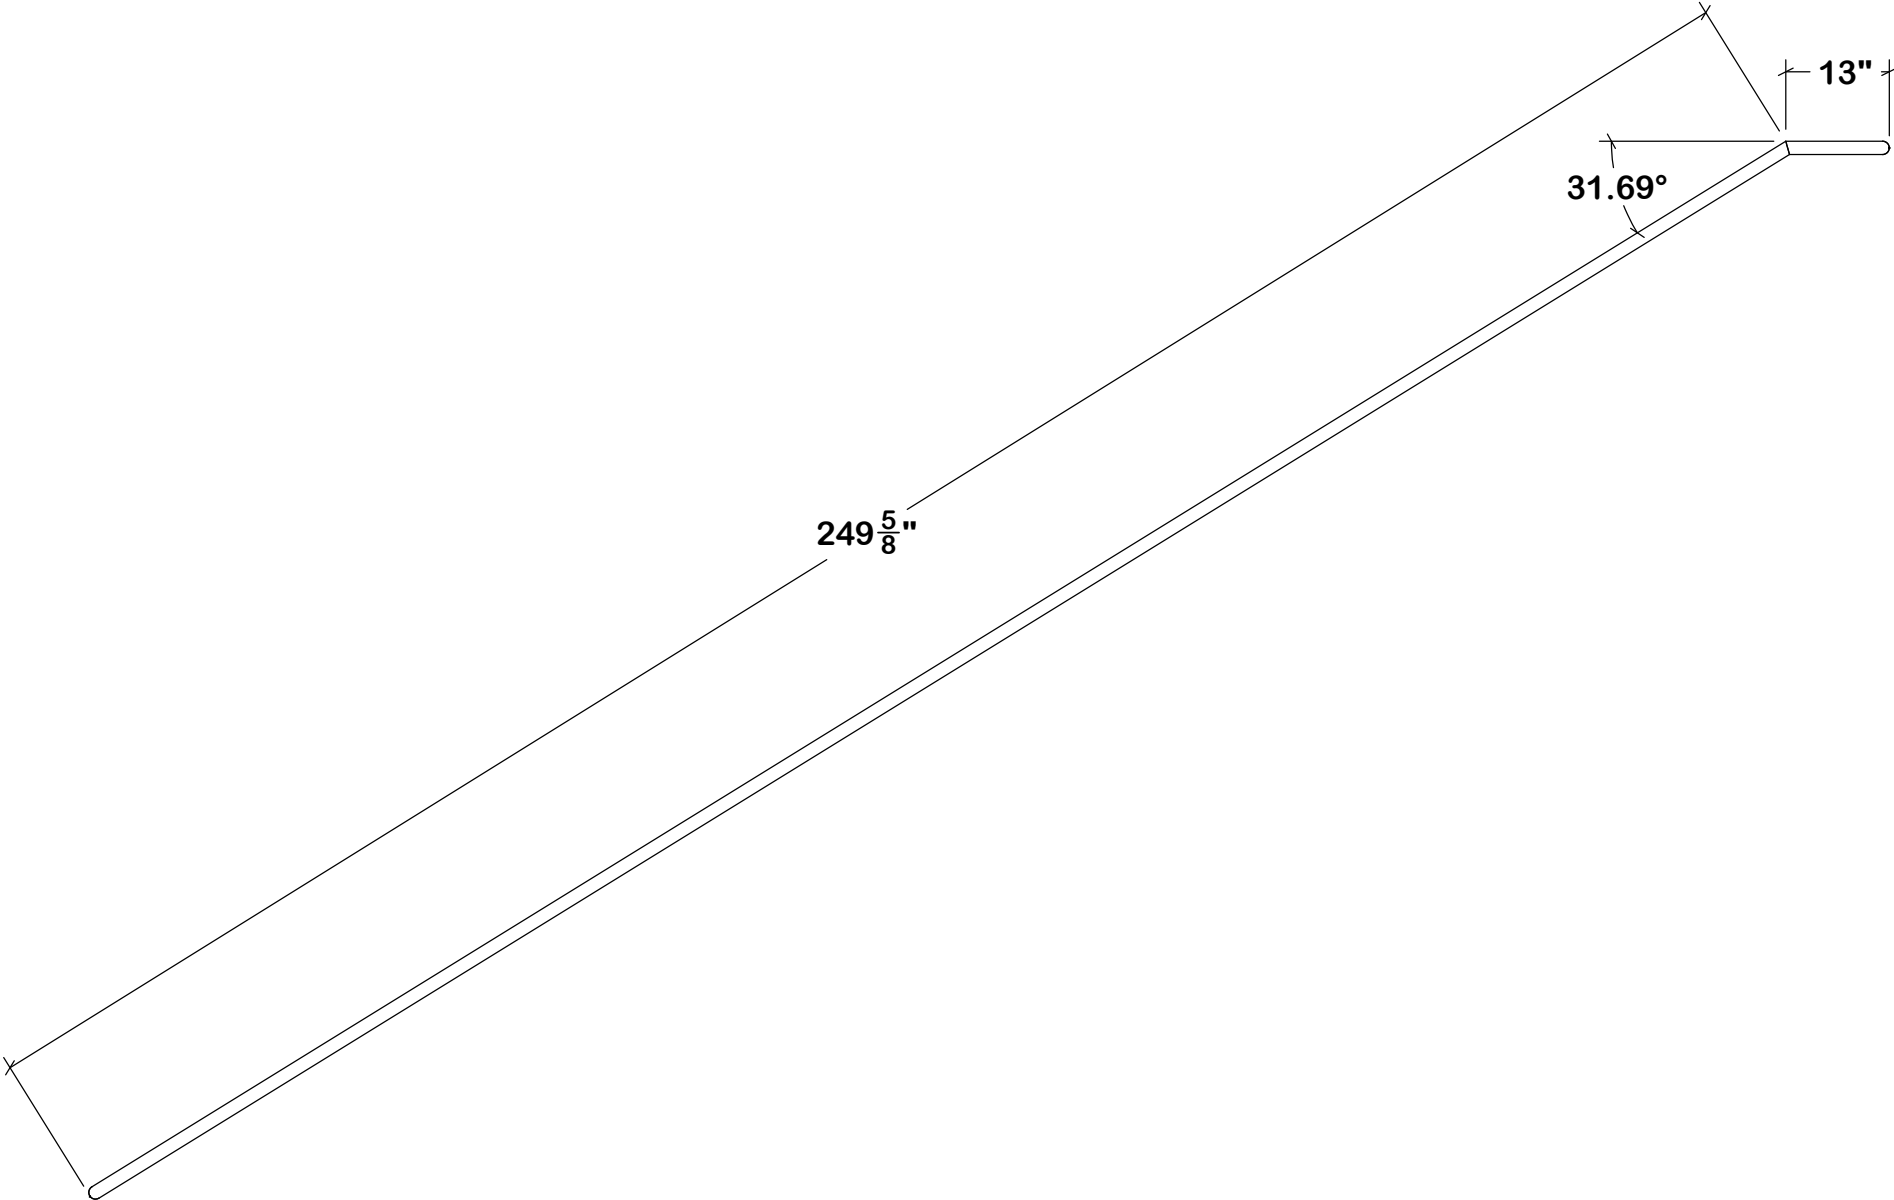

Stair Wallgrab 1 "674-WG1"- QTY (1)

Index	Date	Description	By



Mile High Metal Works, Inc.
7399 Miller Court, Unit A, Frederick, CO 80504
Office 303-485-8283 Fax 303-485-8206

Project Name:

CSI Construction - Flats At Sand Creek

Description:

Bld 3W Stair Core

Date:

6/5/2026

Job #:

590-674

Color:

Red Oxide Primed

By:

DCR


Rev:

0

Drawing:


F9

T:\590 Flats at Sand Creek (CO Springs)\Solidworks\Stairs\Bld 3W Stair Core FAB

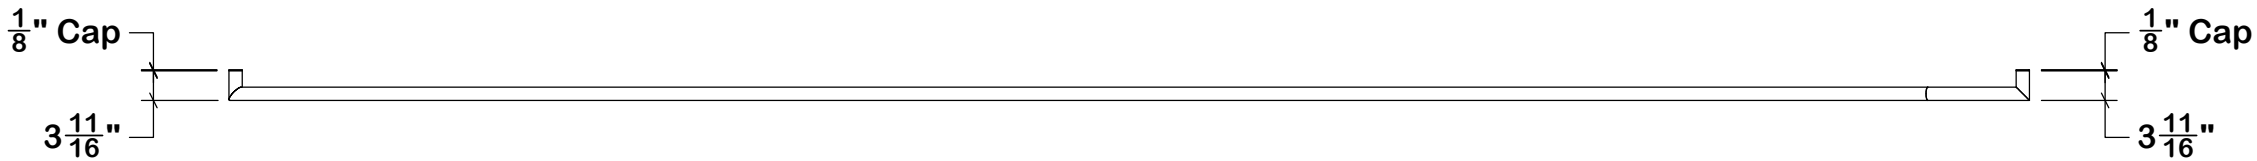

MATERIALS

1-1/4" SCH 10 Pipe

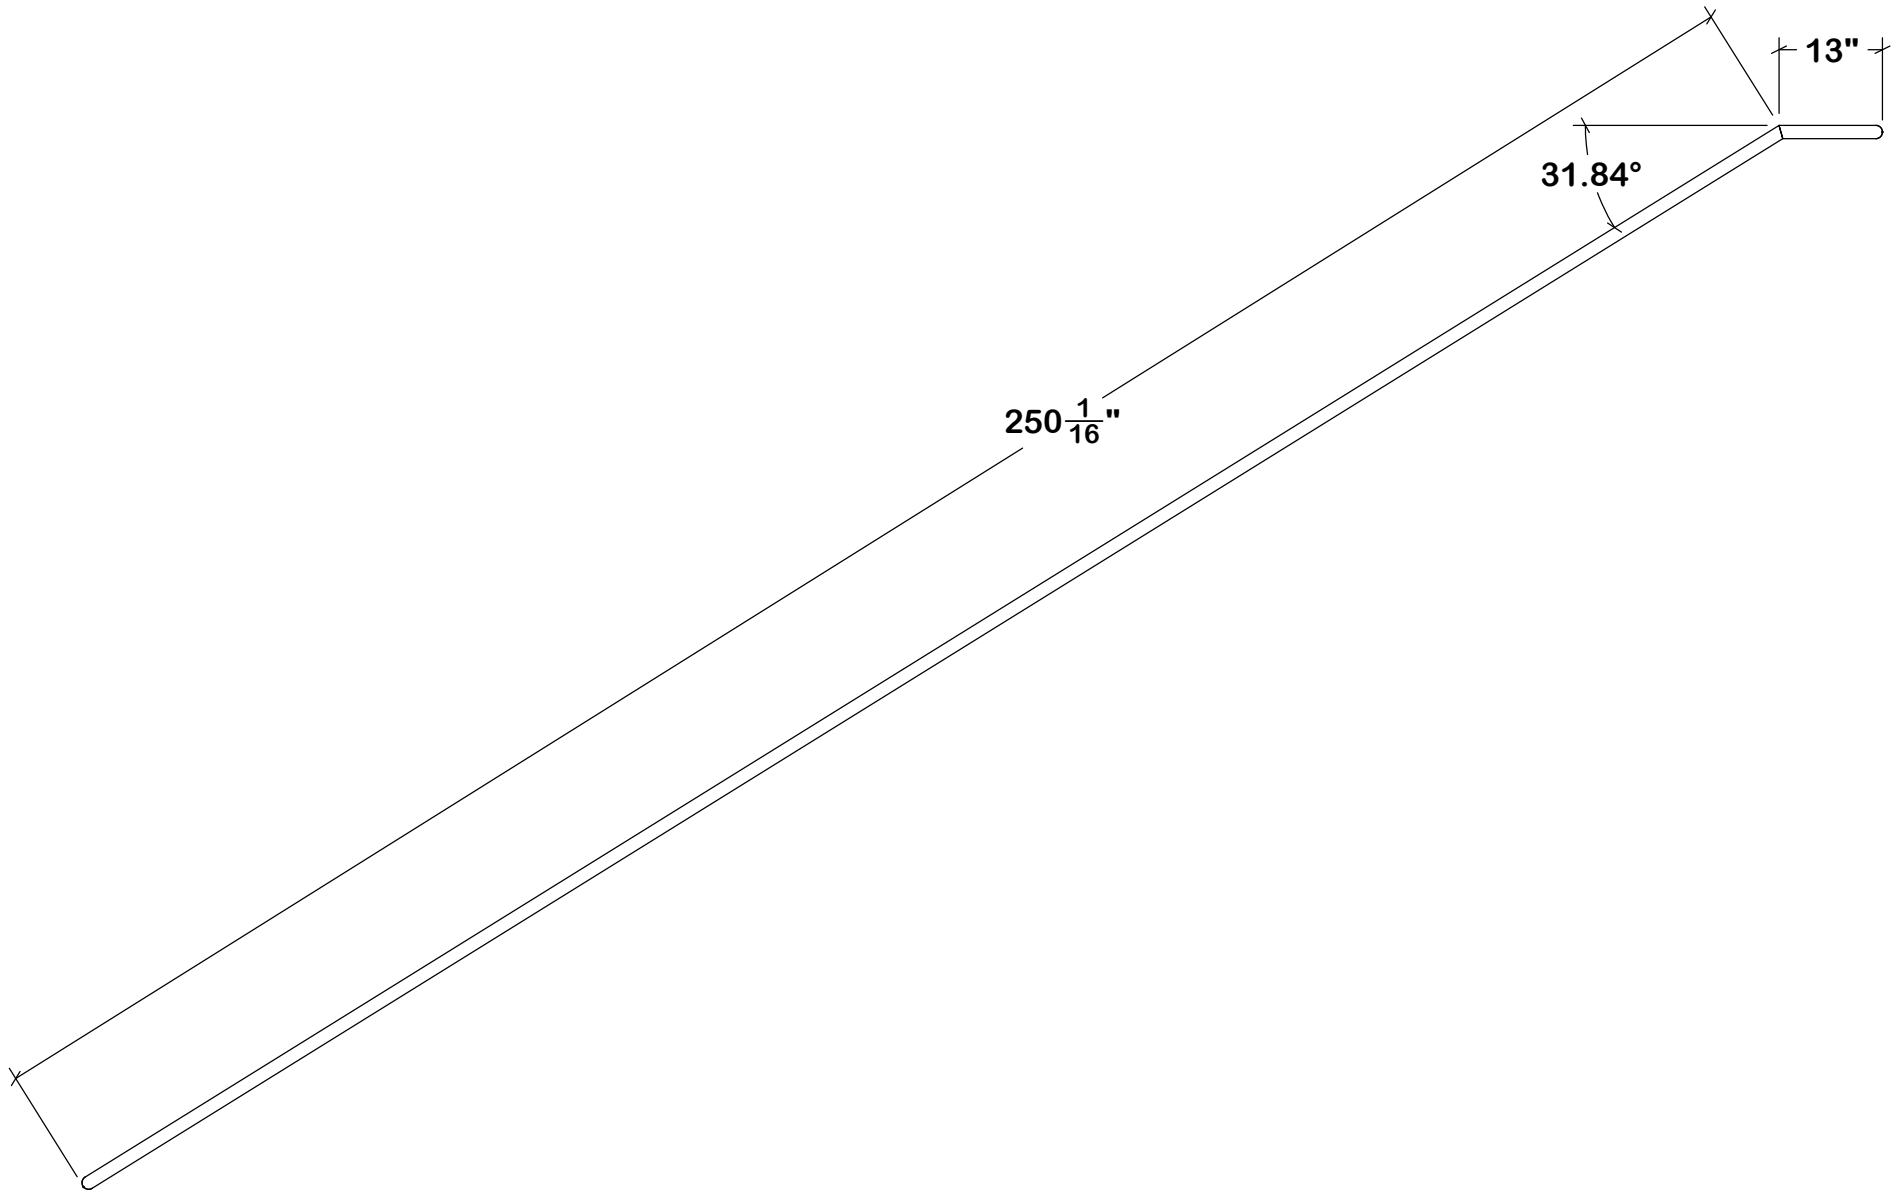

Stair Wallgrab 2 "674-WG2"- QTY (1)

Index	Date	Description	By



Mile High Metal Works, Inc.
7399 Miller Court, Unit A, Frederick, CO 80504
Office 303-485-8283 Fax 303-485-8206

Project Name:

CSI Construction - Flats At Sand Creek

Description:

Bld 3W Stair Core

Date:

6/5/2026

Job #:

590-674

Color:

Red Oxide Primed

By:

DCR


Rev:

0


Drawing:

F10



T:\590 Flats at Sand Creek (CO Springs)\Solidworks\Stairs\Bld 3W Stair Core FAB

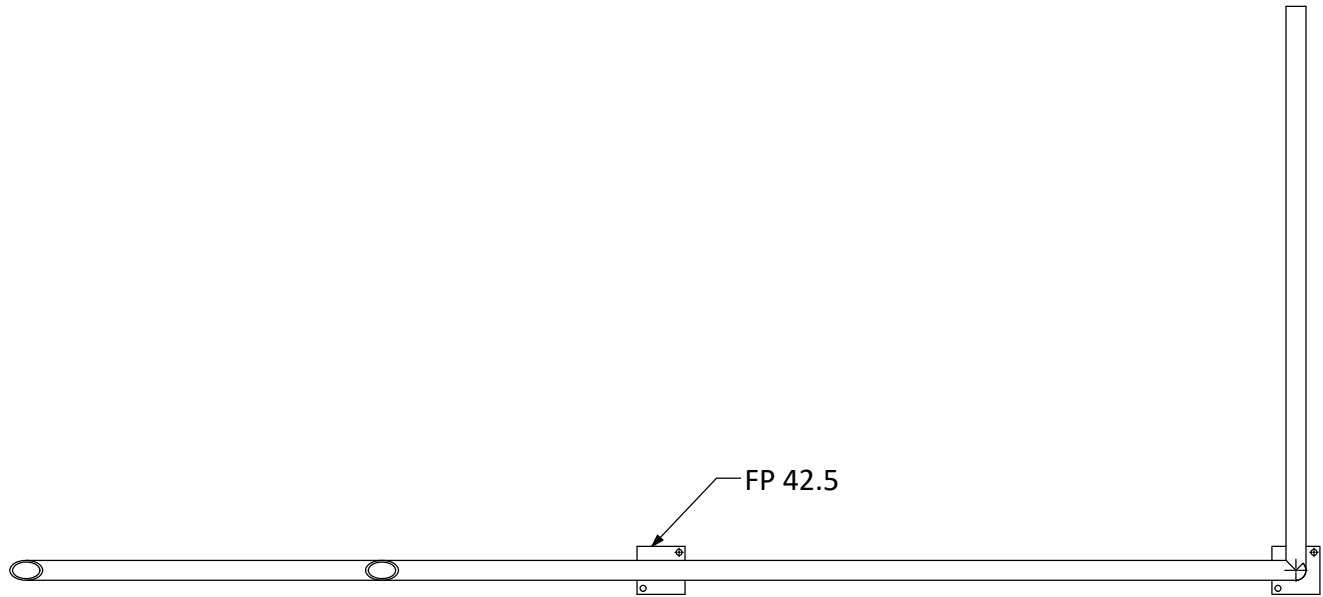

MATERIALS
1-1/4" SCH 10 Pipe

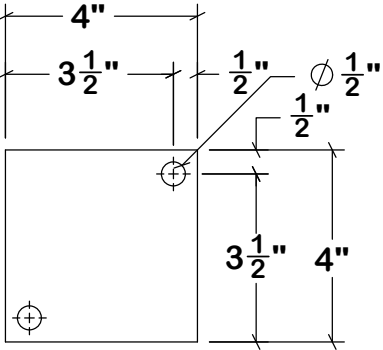

FP 42.5

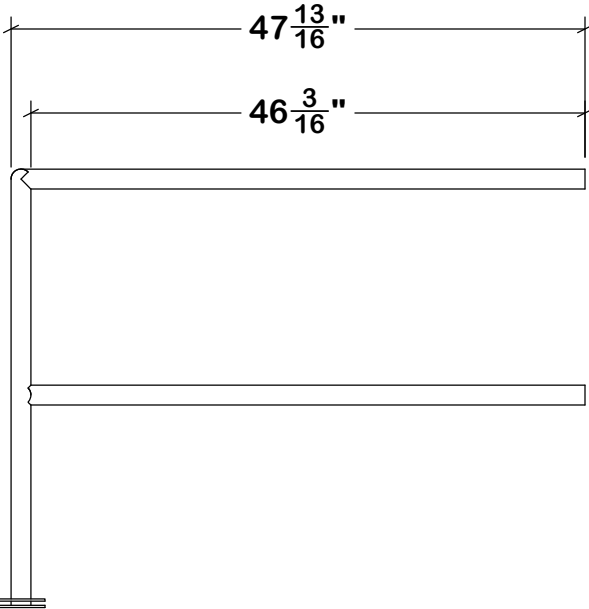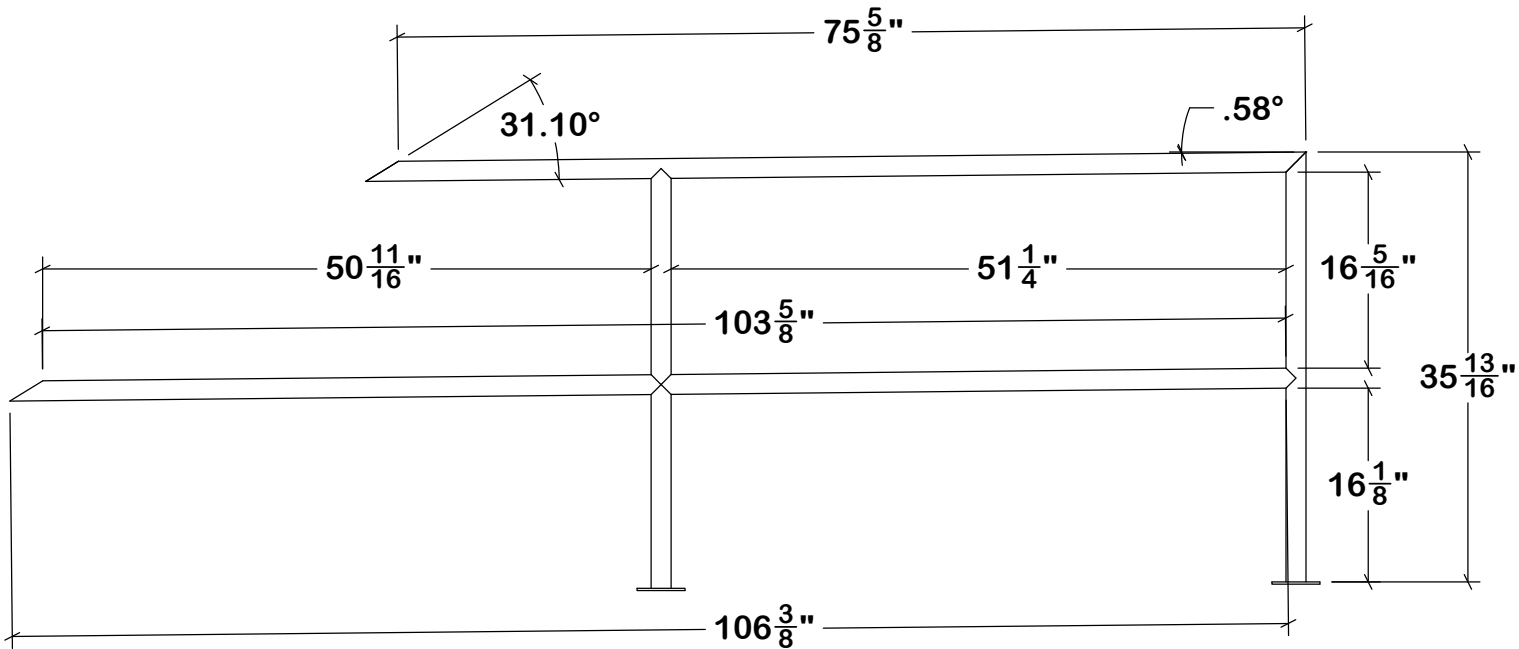

Cane Rail "674-CR1"- QTY (1)

Index	Date	Description	By



Mile High Metal Works, Inc.
7399 Miller Court, Unit A, Frederick, CO 80504
Office 303-485-8283 Fax 303-485-8206

Project Name:
CSI Construction - Flats At
Sand Creek

Description:
Bld 3W Stair Core

Date:
6/5/2026

Job #:
590-674


Color:
Red Oxide
Primed

By:
DCR


Rev:
0

Drawing:
F11

T:\590 Flats at Sand Creek (CO Springs)\Solidworks\Stairs\Bld 3W Stair Core FAB

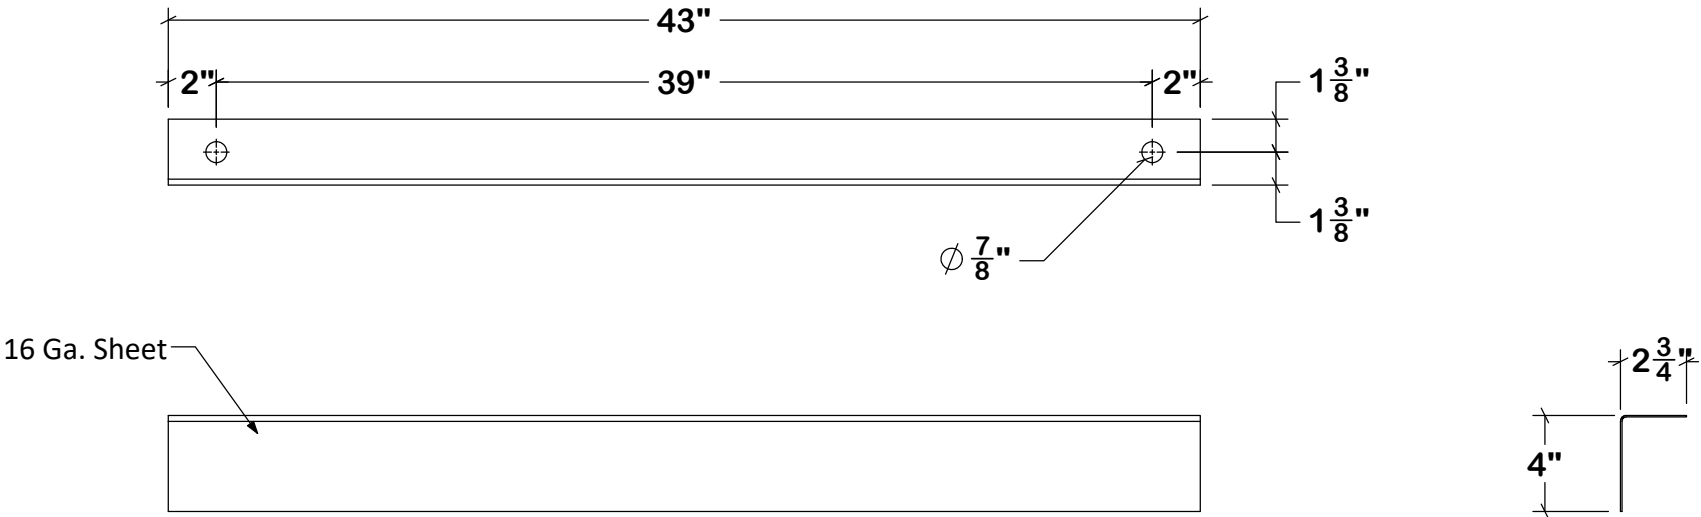

Small Riser Pan - QTY (2)

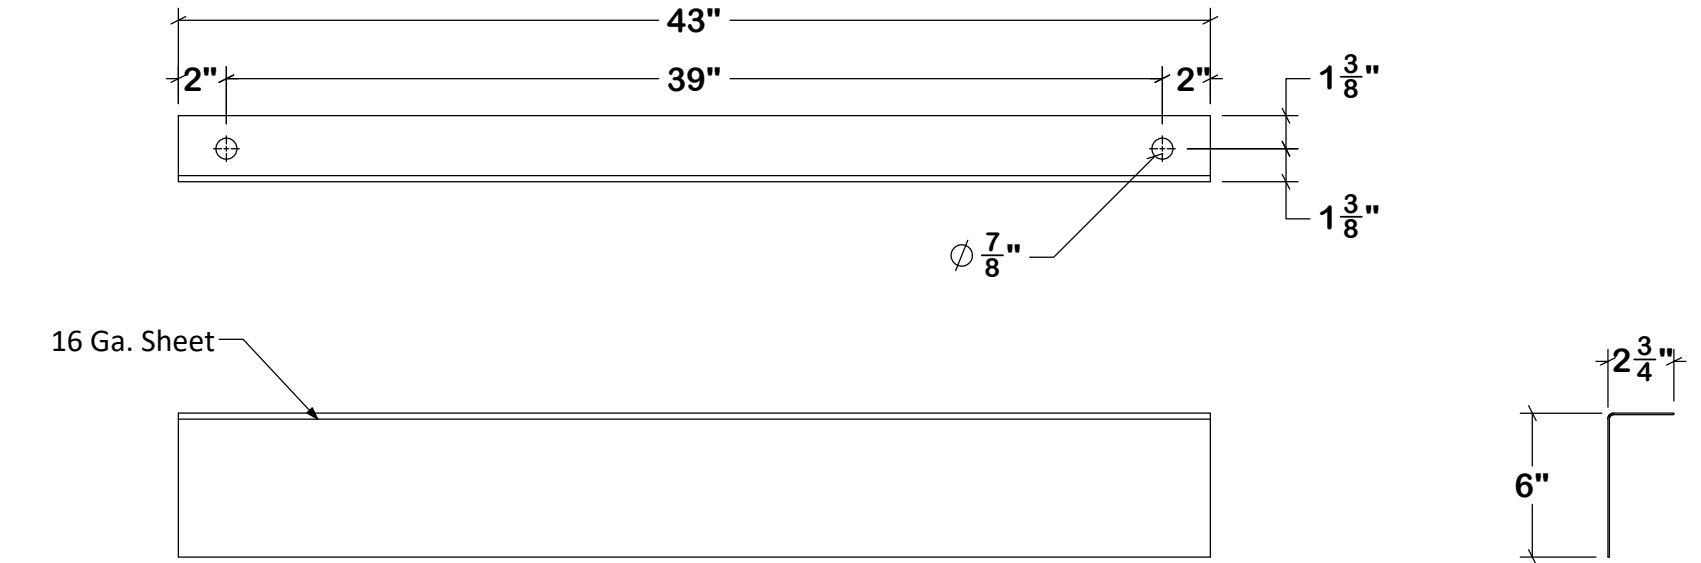

Large Riser Pan - QTY (34)

Index	Date	Description	By



Mile High Metal Works, Inc.
7399 Miller Court, Unit A, Frederick, CO 80504
Office 303-485-8283 Fax 303-485-8206

Project Name:
CSI Construction - Flats At
Sand Creek

Description:
Bld 3W Stair Core

Date:
6/5/2026

Job #:
590-674


Color:
Red Oxide
Primed

By:
DCR


Rev:
0

Drawing:
F12


T:\590 Flats at Sand Creek (CO Springs)\Solidworks\Stairs\Bld 3W Stair Core FAB

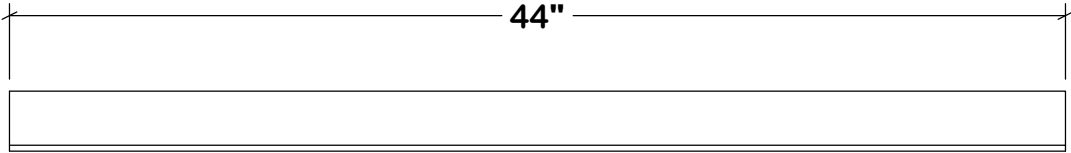


Nosing Angle - QTY (2)

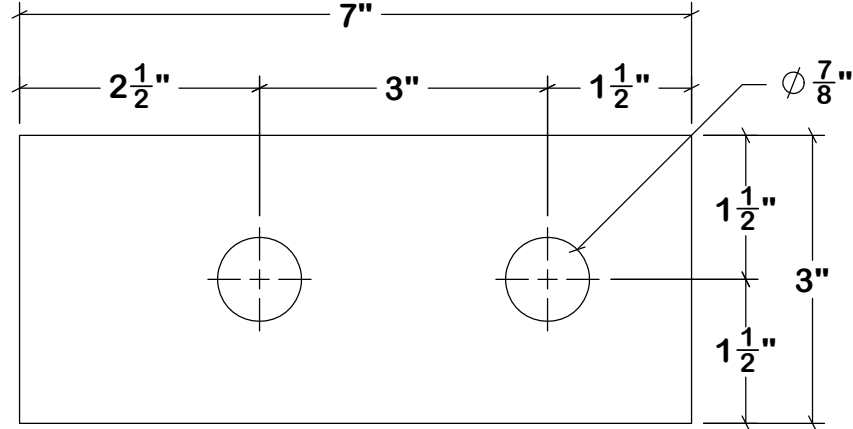


SP7 - QTY (4)

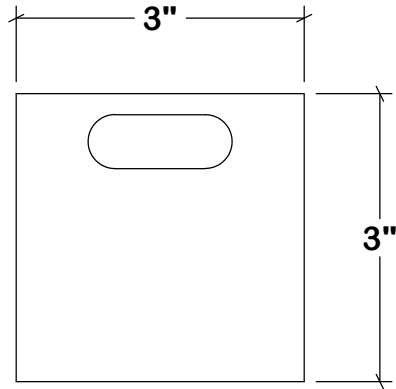


SP3 - QTY (4)

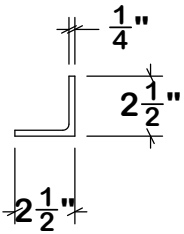


FP 42.5 - QTY (2)

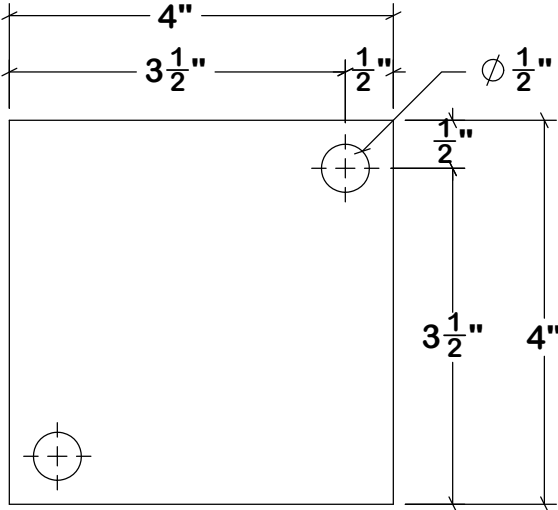

FP 44.5 - QTY (8)

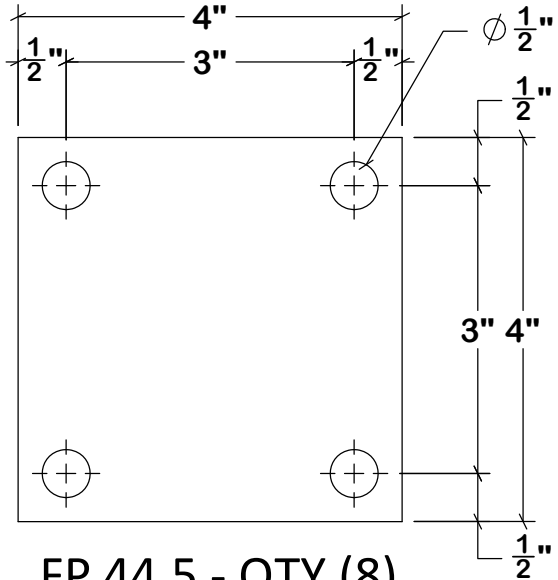

Typ Handrail Bracket - QTY (6)

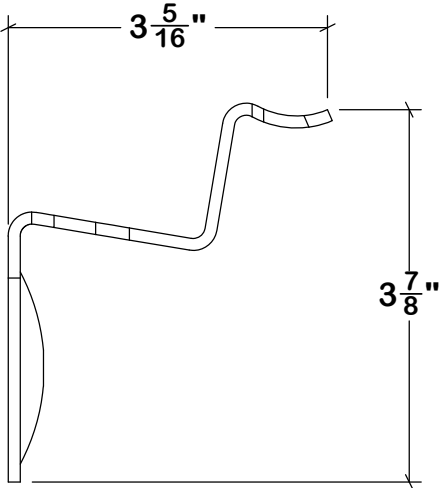

Typ Wallgrab Bracket - QTY (8)

Index	Date	Description	By



Mile High Metal Works, Inc.
7399 Miller Court, Unit A, Frederick, CO 80504
Office 303-485-8283 Fax 303-485-8206

Project Name:
CSI Construction - Flats At
Sand Creek

Description:
Bld 3W Stair Core

Date:
6/5/2026

Job #:
590-674



Color:
Red Oxide
Primed

By:
DCR

Rev:
0

Drawing:
F13

T:\590 Flats at Sand Creek (CO Springs)\Solidworks\Stairs\Bld 3W Stair Core FAB

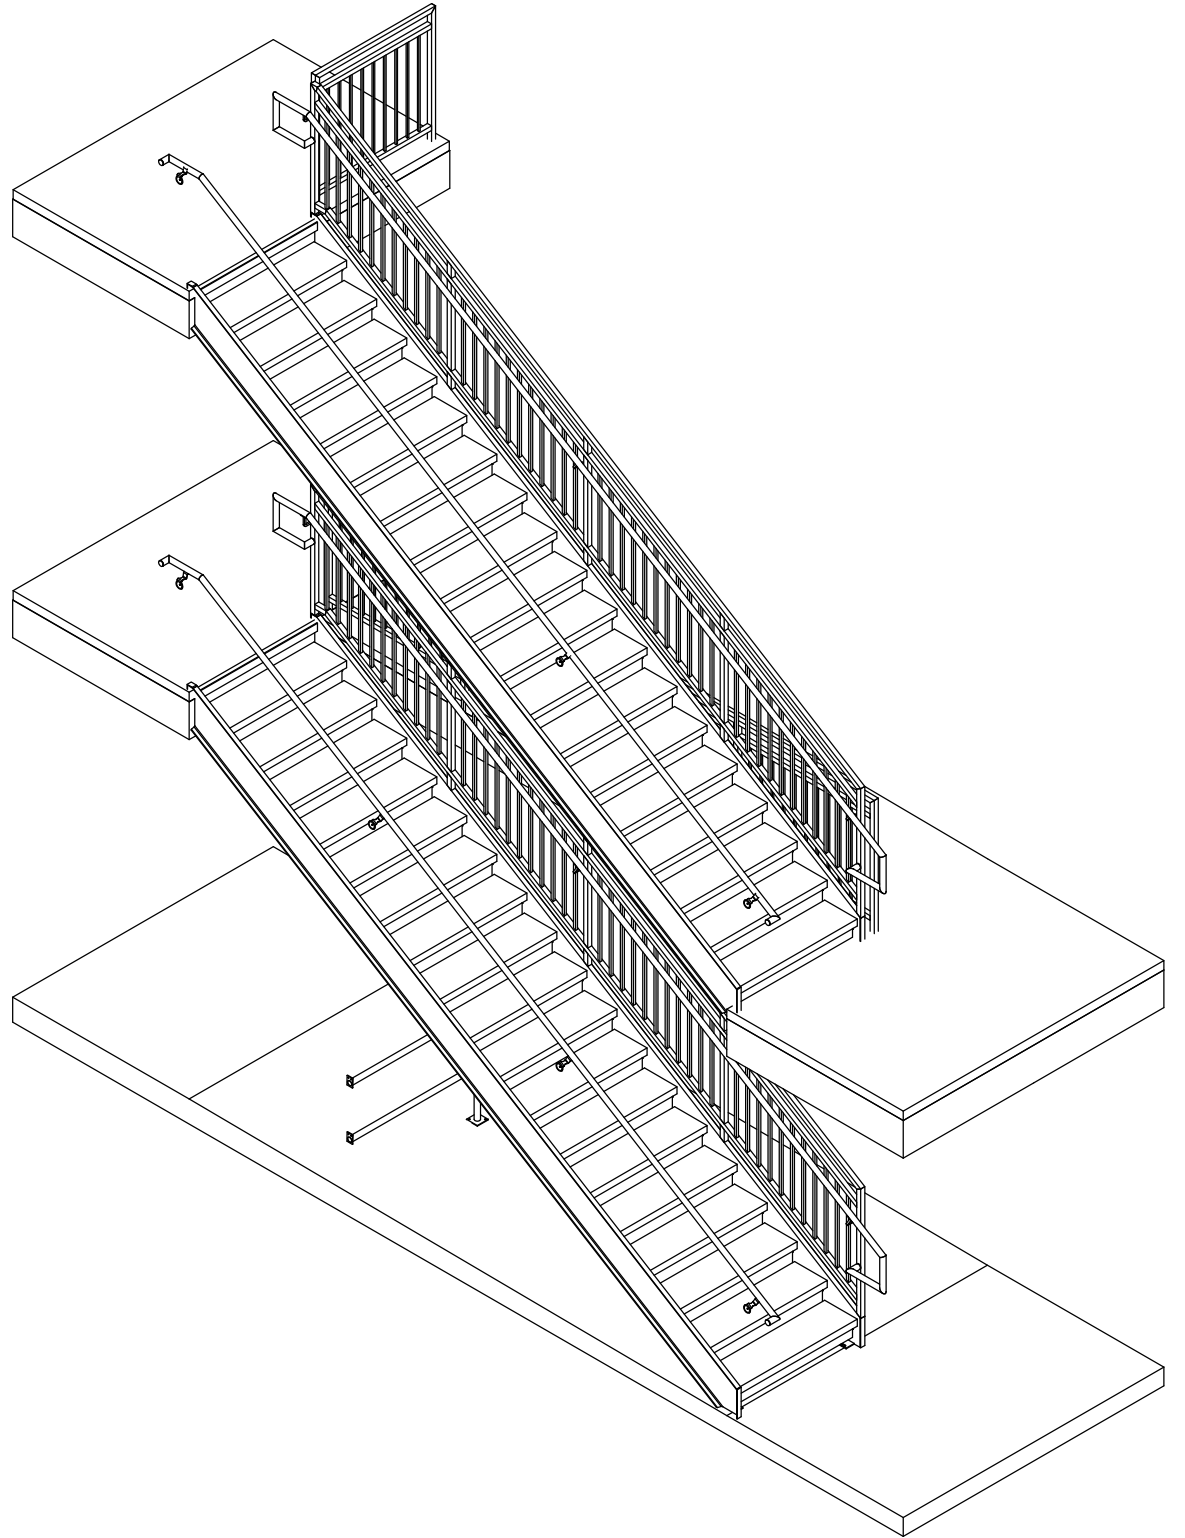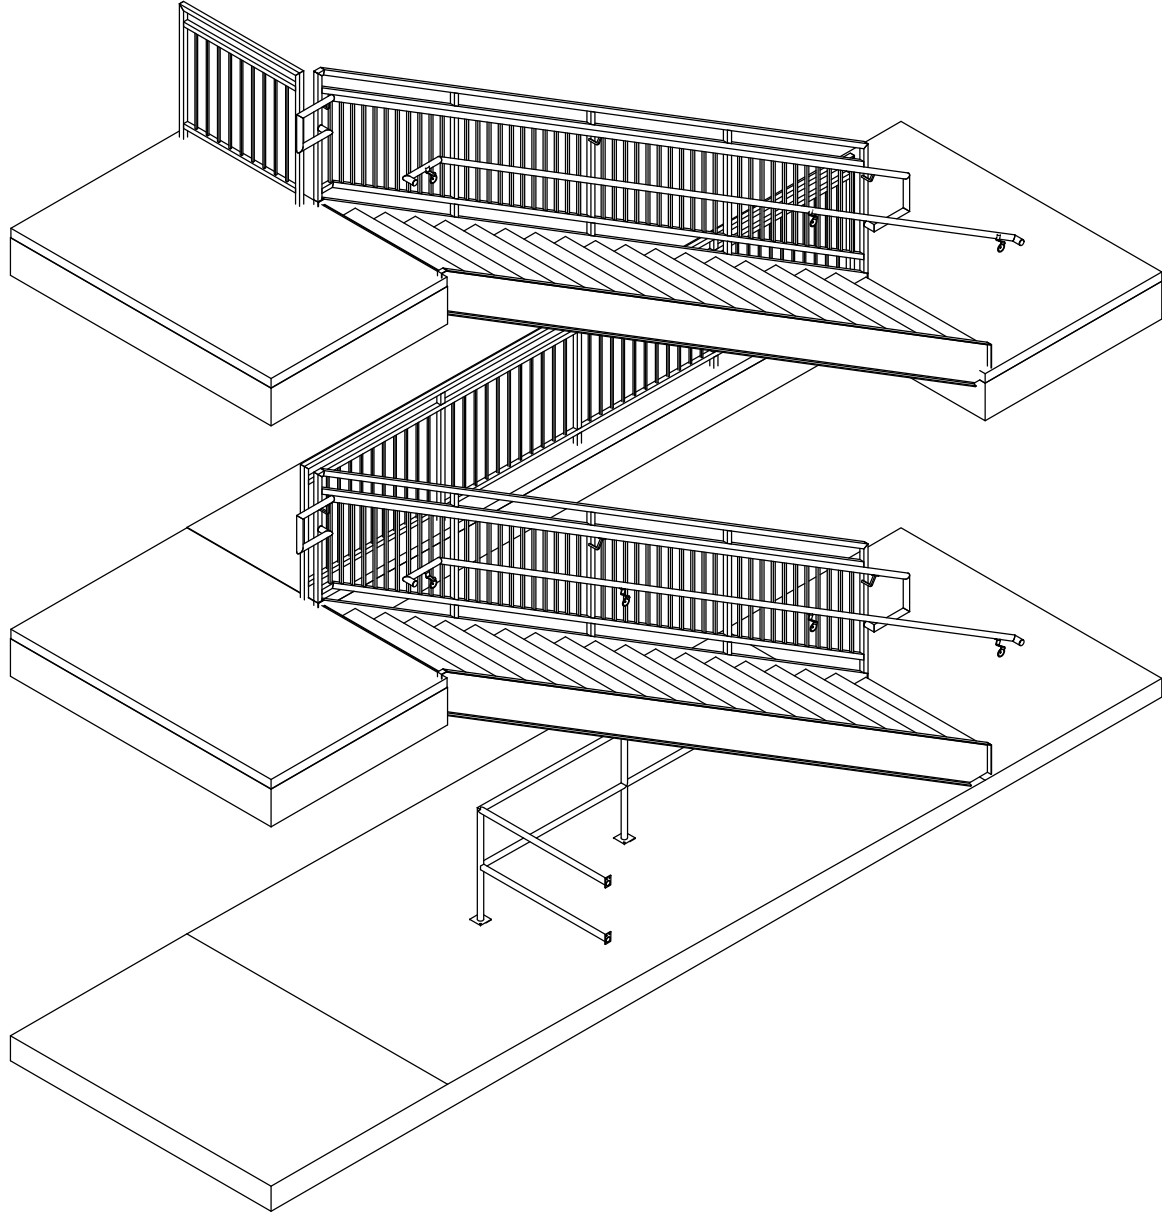

Index	Date	Description	By



Mile High Metal Works, Inc.
7399 Miller Court, Unit A, Frederick, CO 80504
Office 303-485-8283 Fax 303-485-8206

Project Name:
CSI Construction - Flats At
Sand Creek

Description:
Bld 3W Stair Core

Date:
6/5/2026

Job #:
590-674



Color:
Red Oxide
Primed

By:
DCR

Rev:
0

Drawing:
F14

T:\590 Flats at Sand Creek (CO Springs)\Solidworks\Stairs\Bld 3W Stair Core FAB

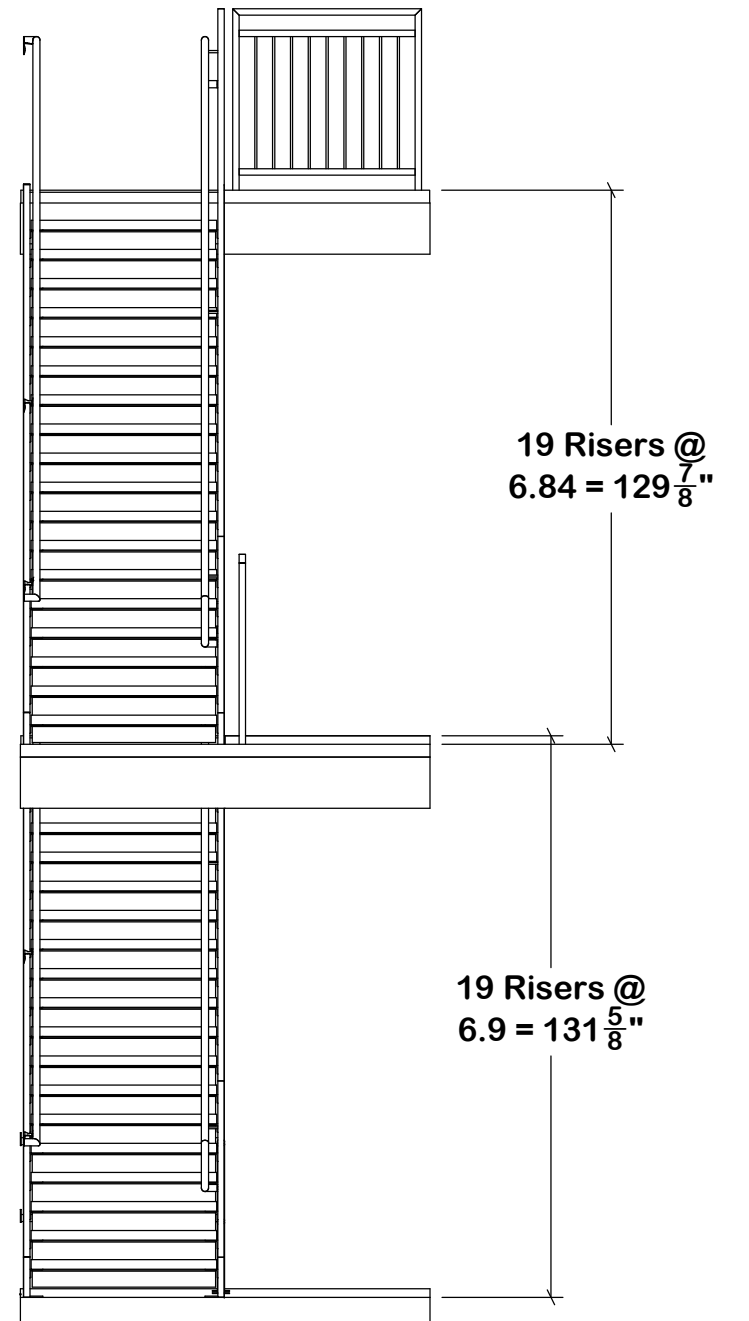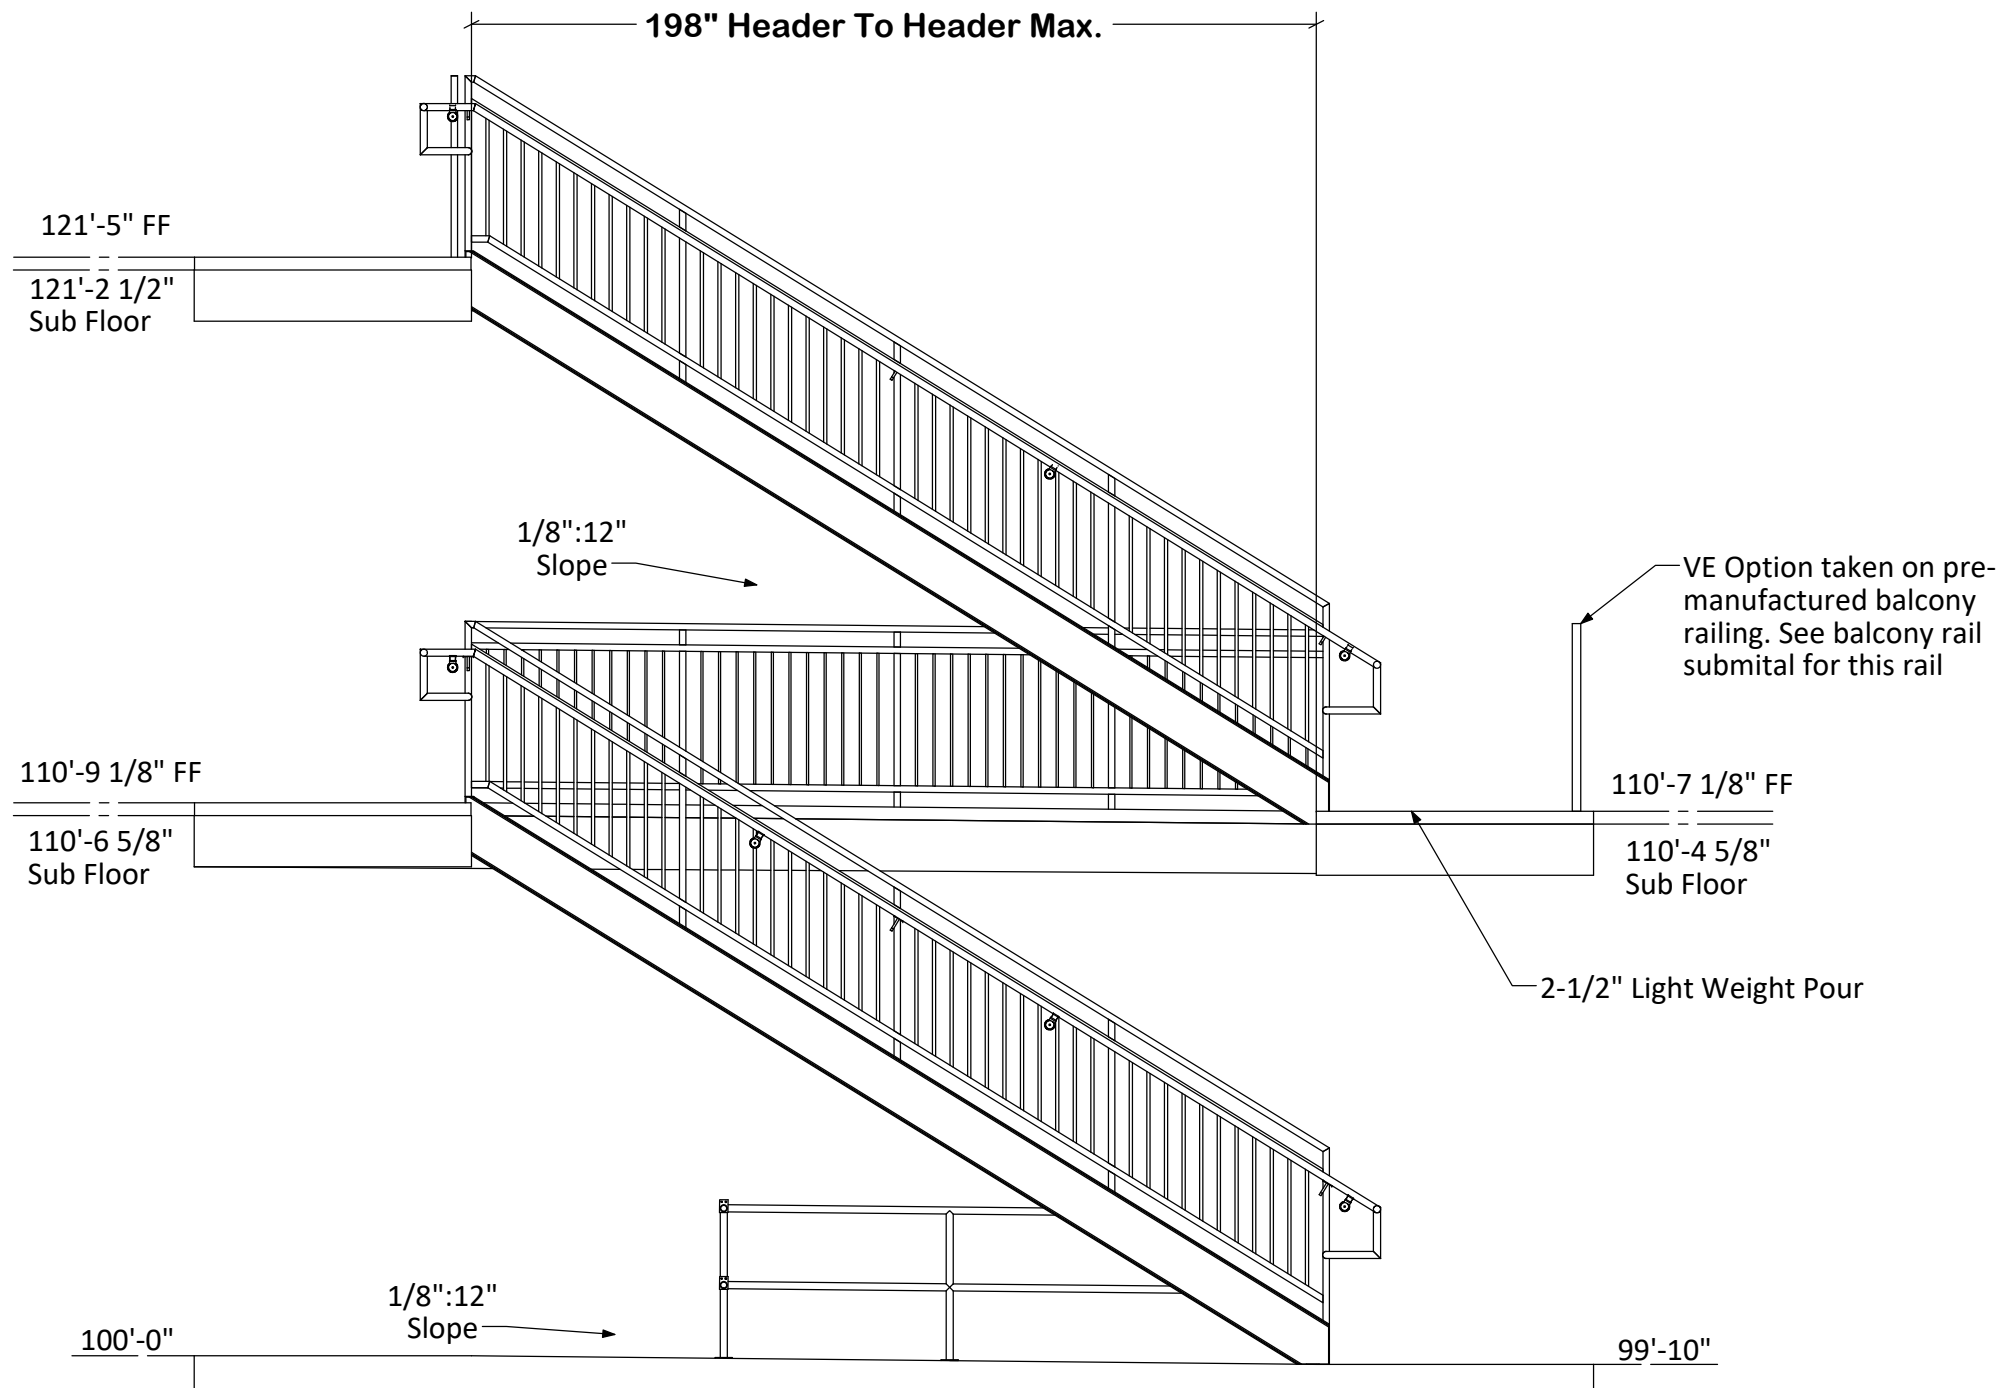

Index	Date	Description	By



Mile High Metal Works, Inc.
7399 Miller Court, Unit A, Frederick, CO 80504
Office 303-485-8283 Fax 303-485-8206

Project Name:

CSI Construction - Flats At Sand Creek

Description:

Bld 3W Stair Core

Date:

6/5/2026

Job #:

590-674

Color:

Red Oxide Primed

By:

DCR




Rev:

0

Drawing:

F15

T:\590 Flats at Sand Creek (CO Springs)\Solidworks\Stairs\Bld 3W Stair Core FAB

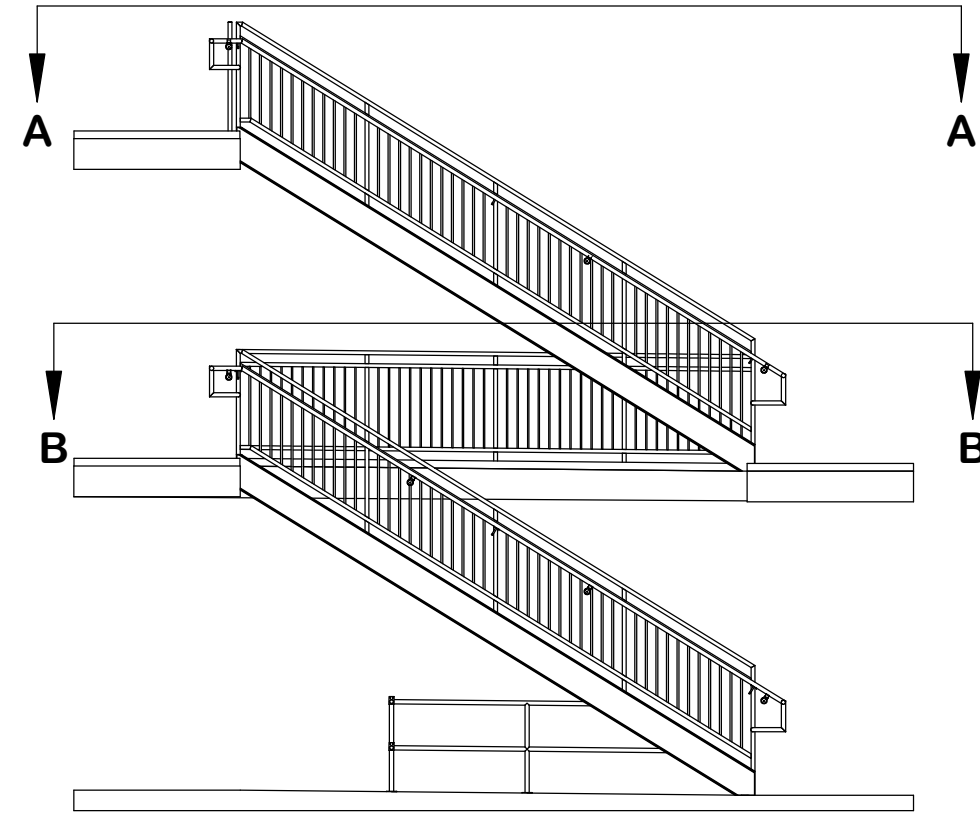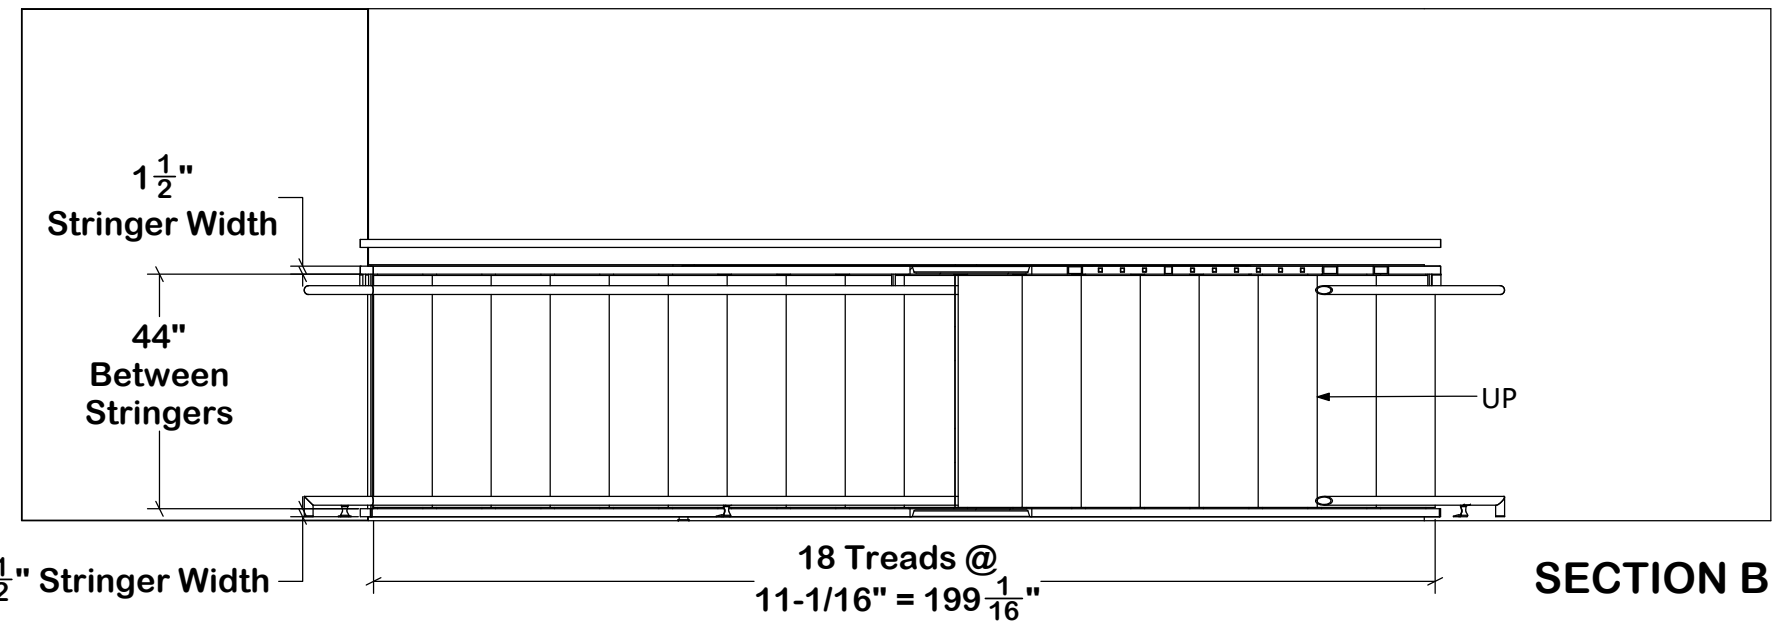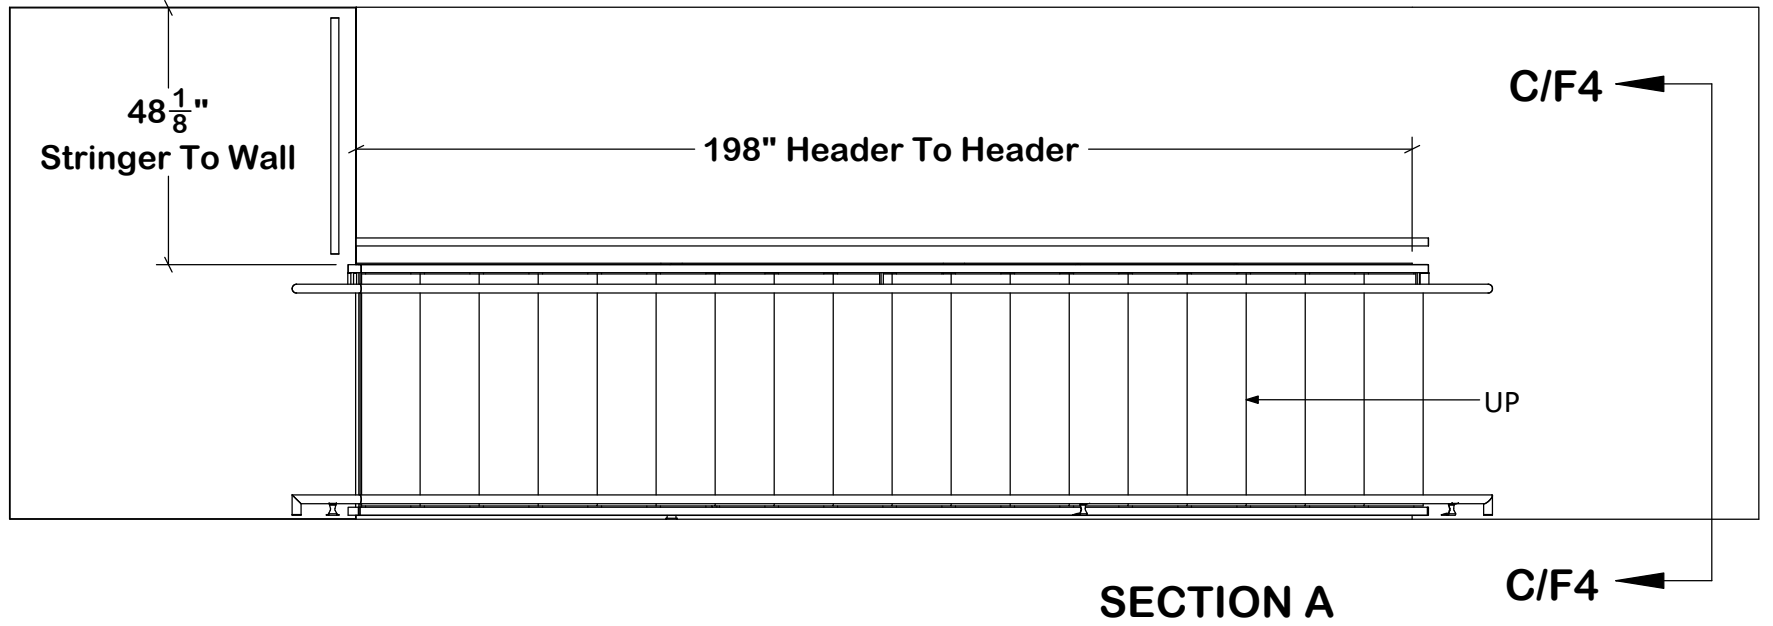

Index	Date	Description	By


Mile High Metal Works, Inc.
7399 Miller Court, Unit A, Frederick, CO 80504
Office 303-485-8283 Fax 303-485-8206

Project Name:
CSI Construction - Flats At
Sand Creek

Description:
Bld 3W Stair Core

Date:
6/5/2026

Job #:
590-674


Color:
Red Oxide
Primed

By:
DCR

Rev:
0

Drawing:
F16

T:\590 Flats at Sand Creek (CO Springs)\Solidworks\Stairs\Bld 3W Stair Core FAB

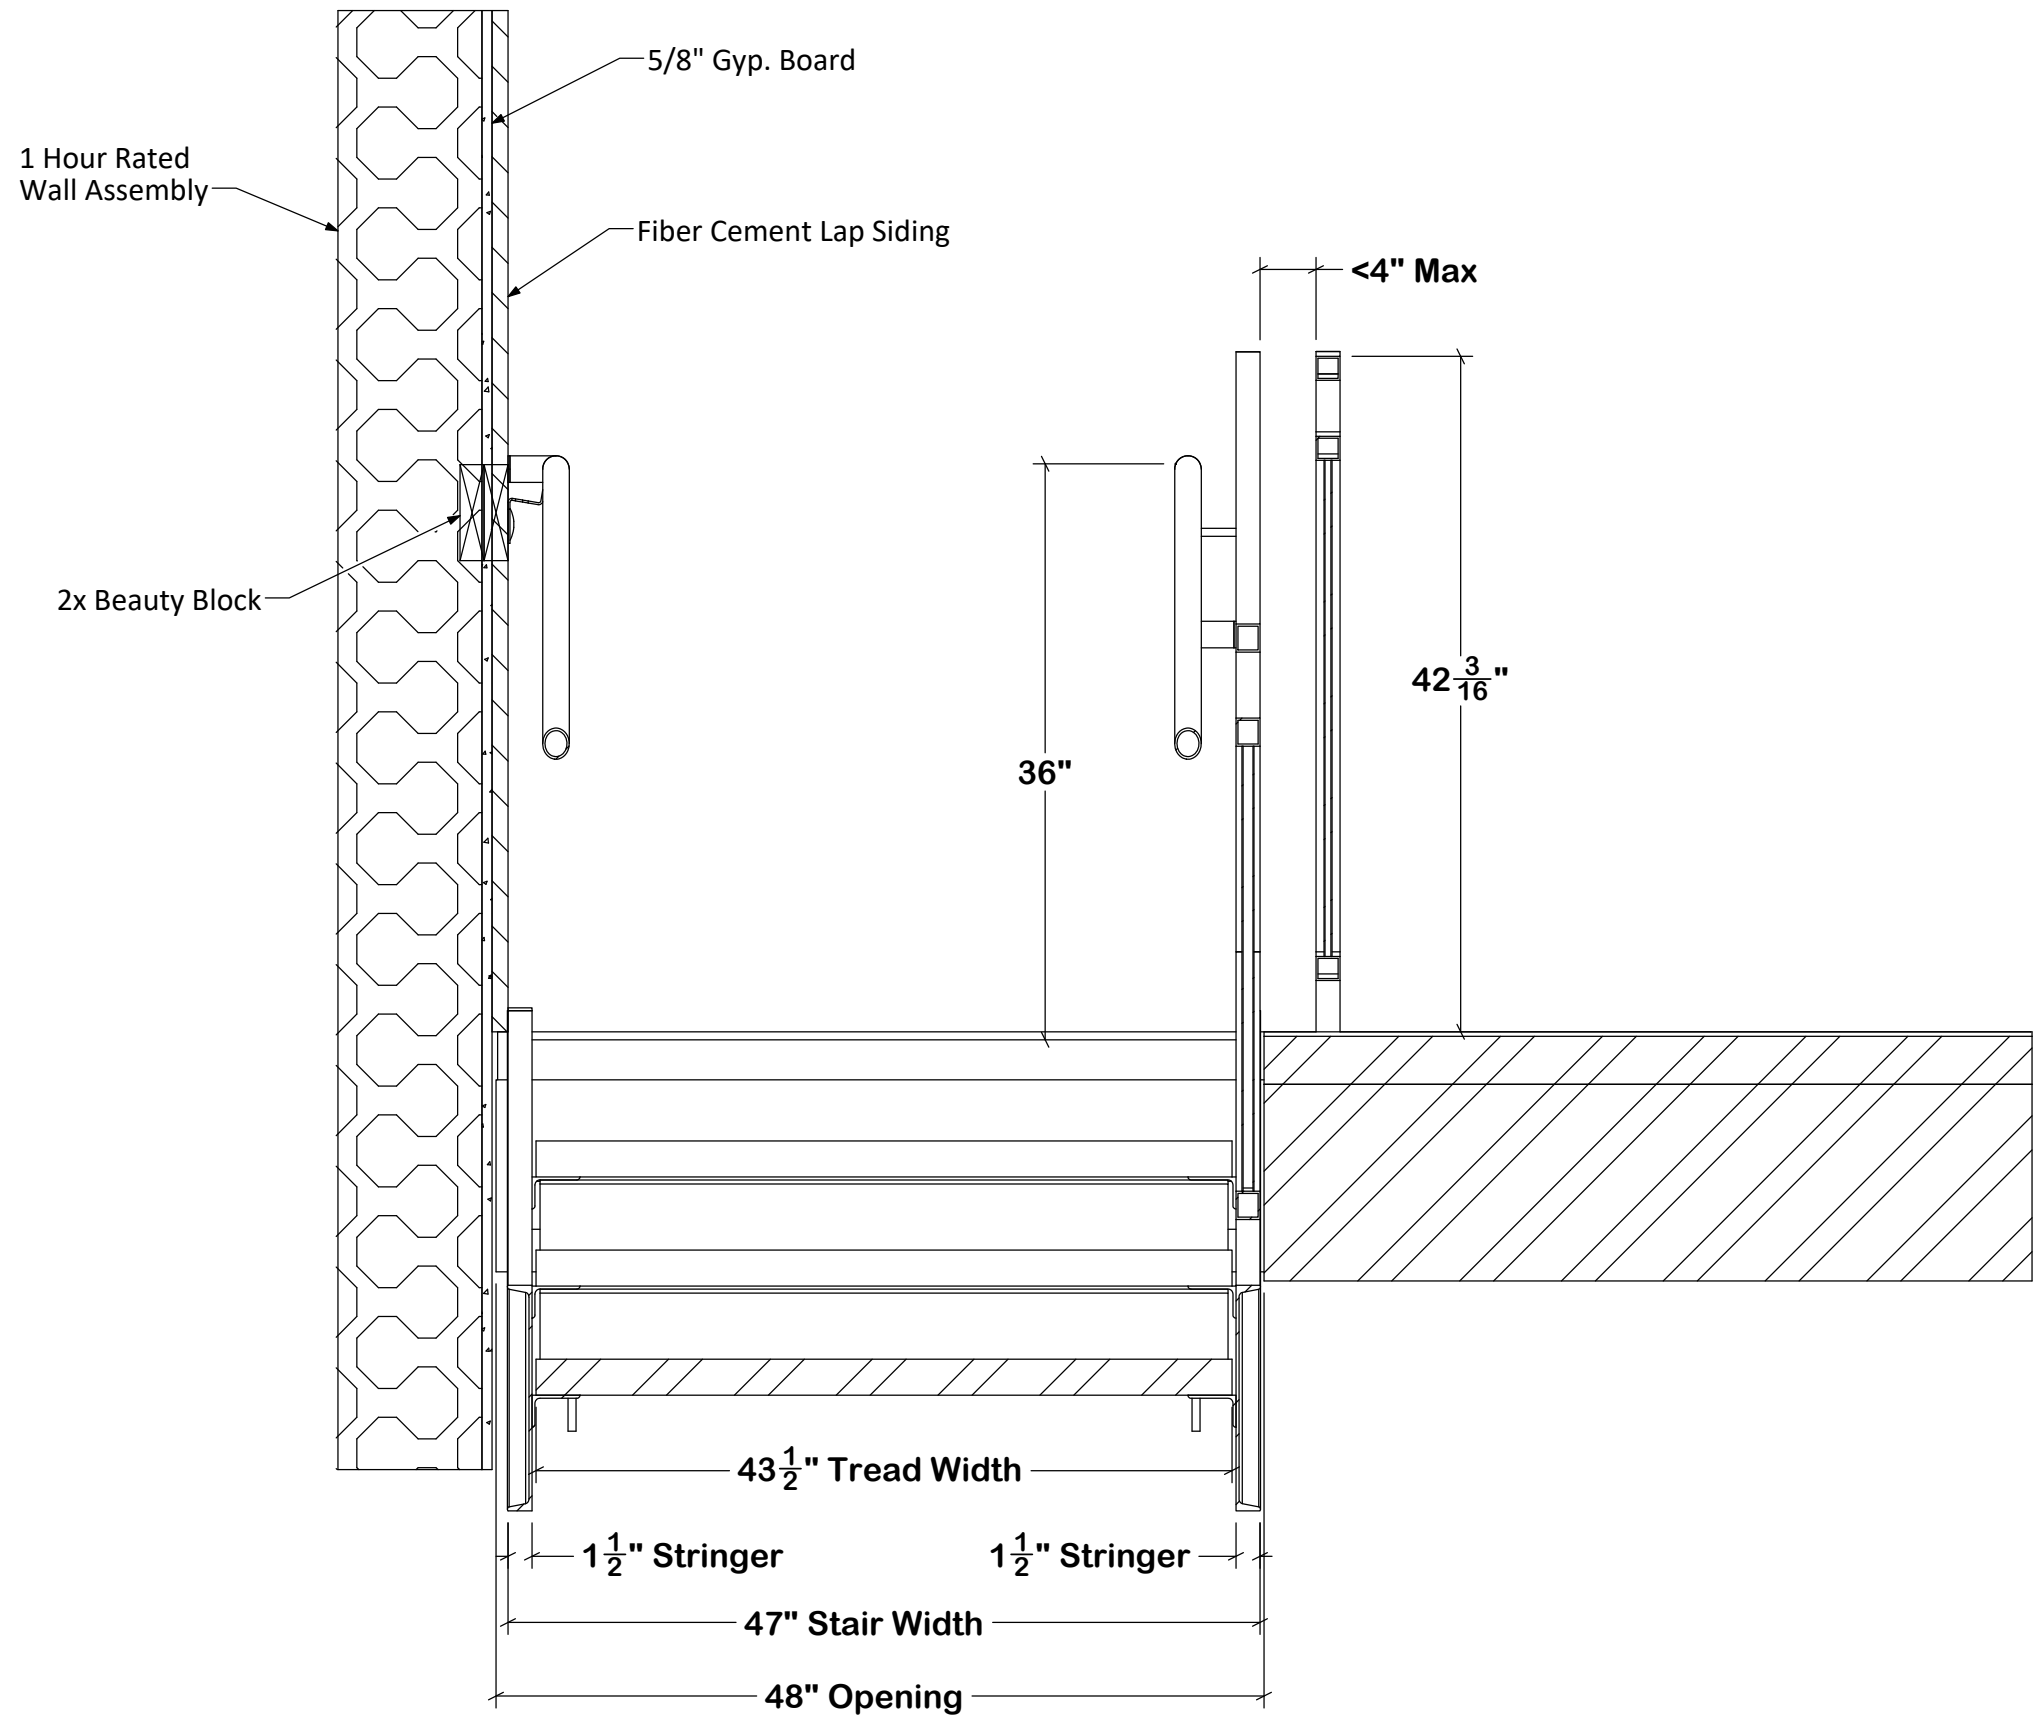

Index	Date	Description	By


Mile High Metal Works, Inc.
7399 Miller Court, Unit A, Frederick, CO 80504
Office 303-485-8283 Fax 303-485-8206

Project Name:
CSI Construction - Flats At
Sand Creek

Description:
Bld 3W Stair Core

Date:
6/5/2026

Job #:
590-674


Color:
Red Oxide
Primed

By:
DCR

Rev:
0

Drawing:
F17


T:\590 Flats at Sand Creek (CO Springs)\Solidworks\Stairs\Bld 3W Stair Core FAB

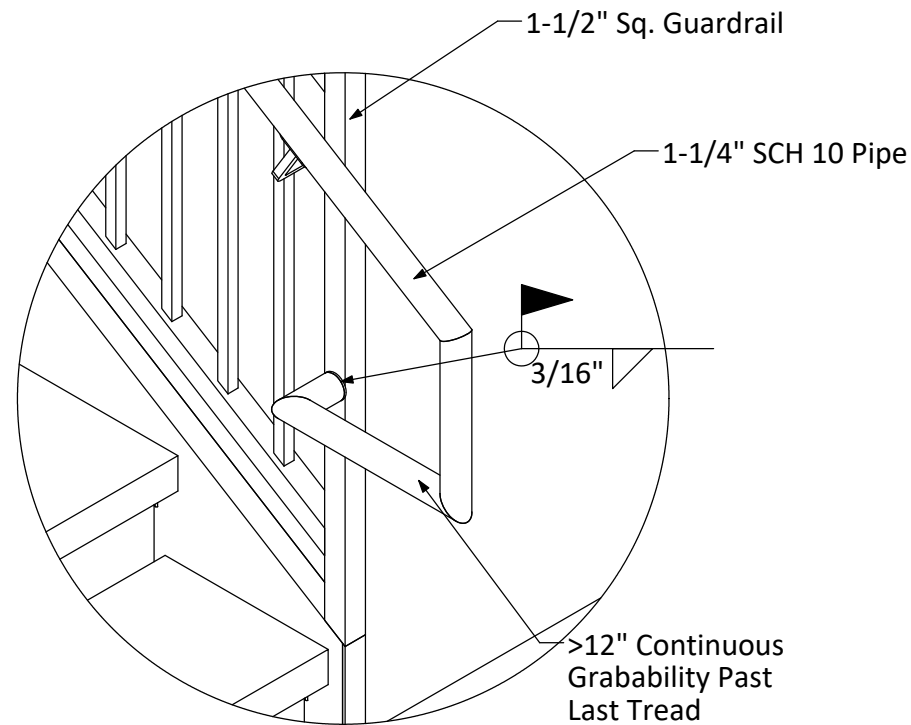


Bottom Handgrab Connection

7"x3"x1/2" Header Plate
Connect To Header W/
(2) 3/4"Ø A307 Thru Bolts


1-1/2"x2-1/2"x1/4"
Mud Dam Angle

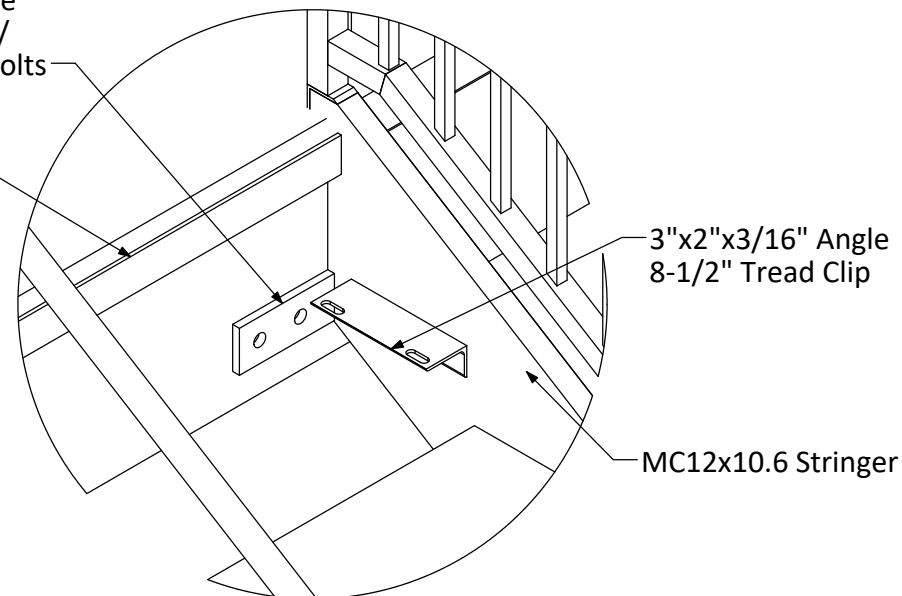

Header Connection

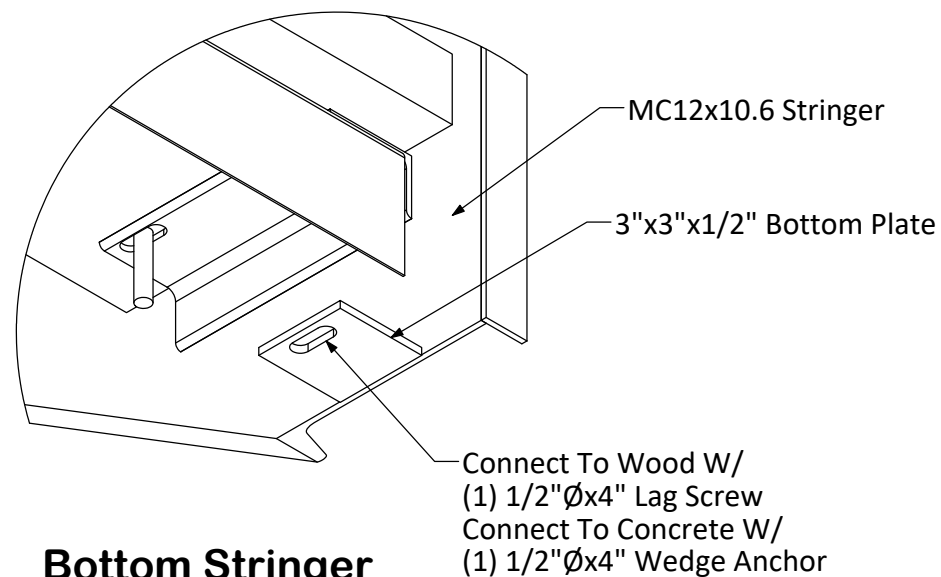

Bottom Stringer Connection

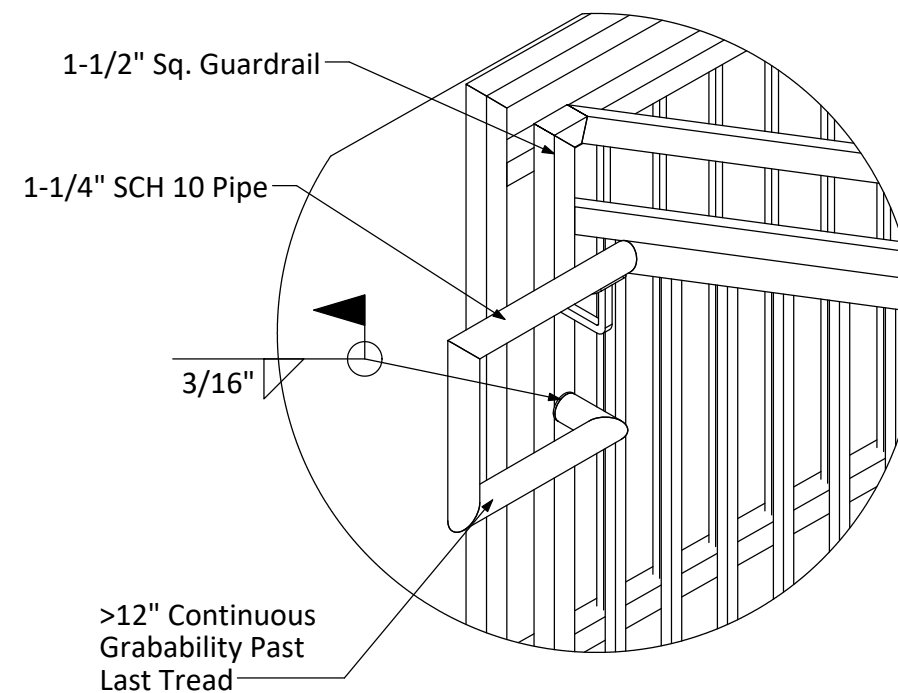

Top Handgrab Connection

Index	Date	Description	By


Mile High Metal Works, Inc.
7399 Miller Court, Unit A, Frederick, CO 80504
Office 303-485-8283 Fax 303-485-8206

Project Name:
CSI Construction - Flats At
Sand Creek

Description:
Bld 3W Stair Core

Date:
6/5/2026

Job #:
590-674


Color:
Red Oxide
Primed

By:
DCR

Rev:
0

Drawing:
F18

T:\590 Flats at Sand Creek (CO Springs)\Solidworks\Stairs\Bld 3W Stair Core FAB

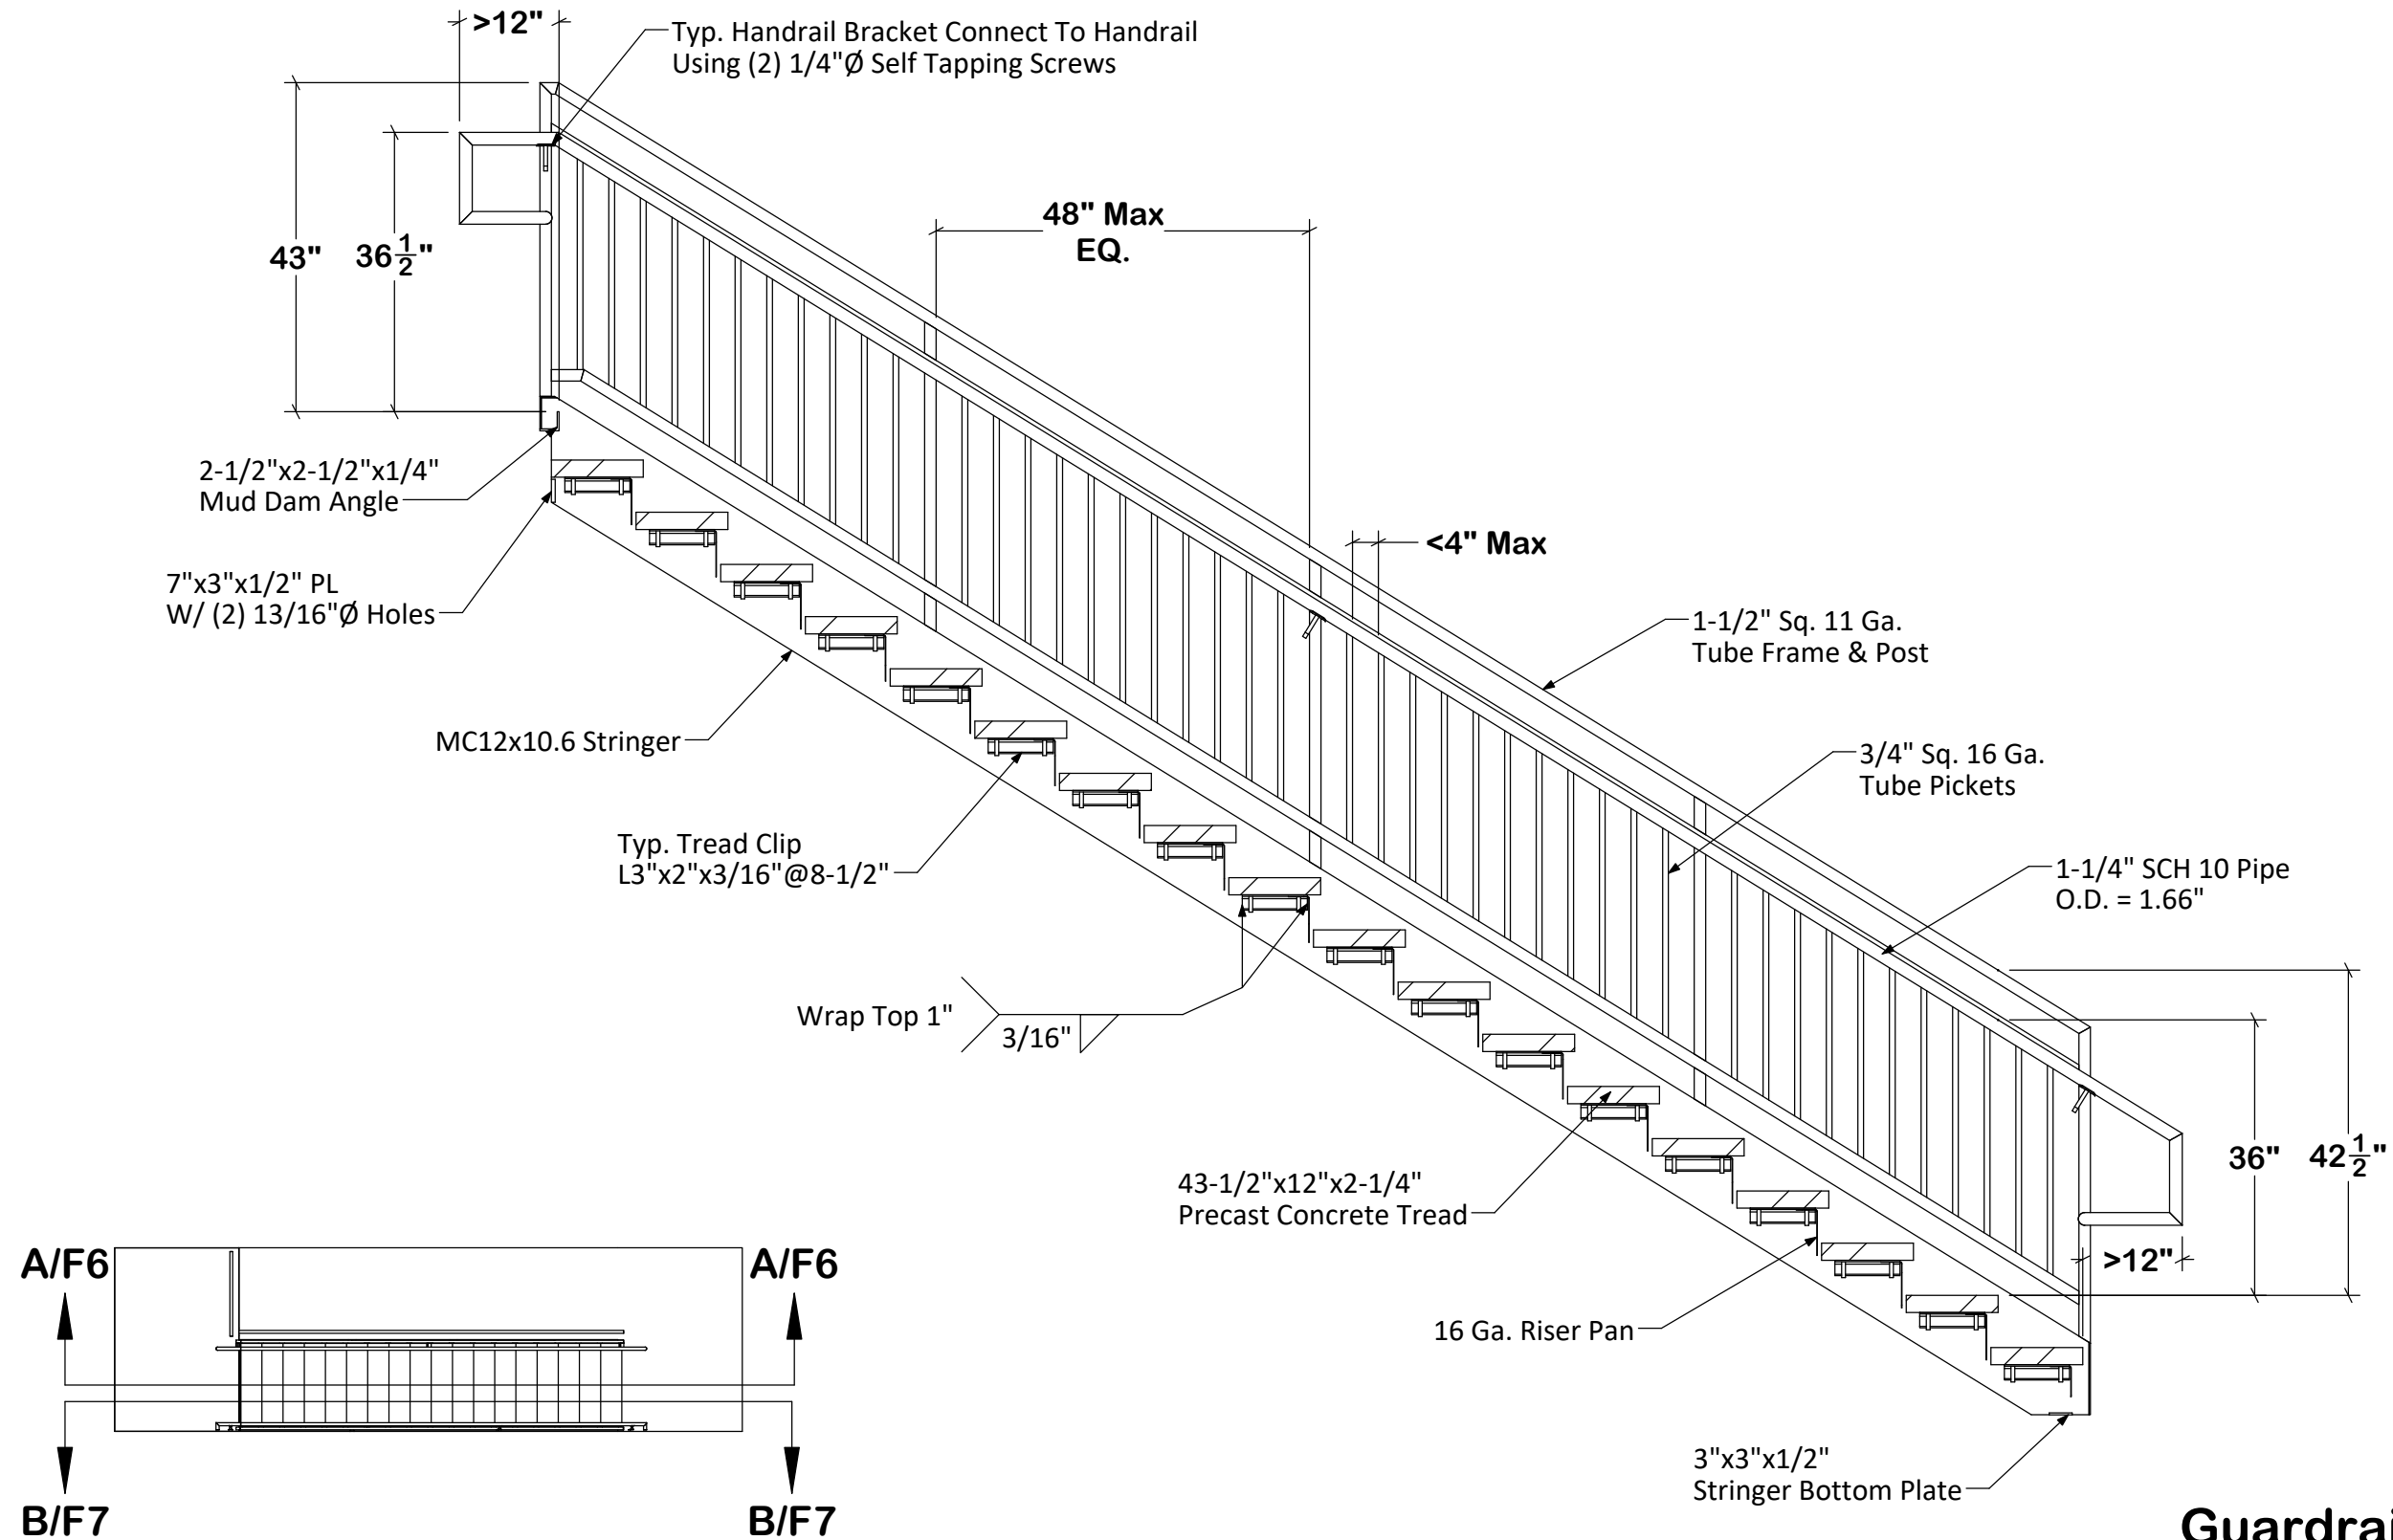

Guardrail Details Typ.

Index	Date	Description	By



Mile High Metal Works, Inc.
7399 Miller Court, Unit A, Frederick, CO 80504
Office 303-485-8283 Fax 303-485-8206

Project Name:
CSI Construction - Flats At
Sand Creek

Description:
Bld 3W Stair Core

Date:
6/5/2026

Job #:
590-674


Color:
Red Oxide
Primed

By:
DCR

Rev:
0

Drawing:
F19

T:\590 Flats at Sand Creek (CO Springs)\Solidworks\Stairs\Bld 3W Stair Core FAB

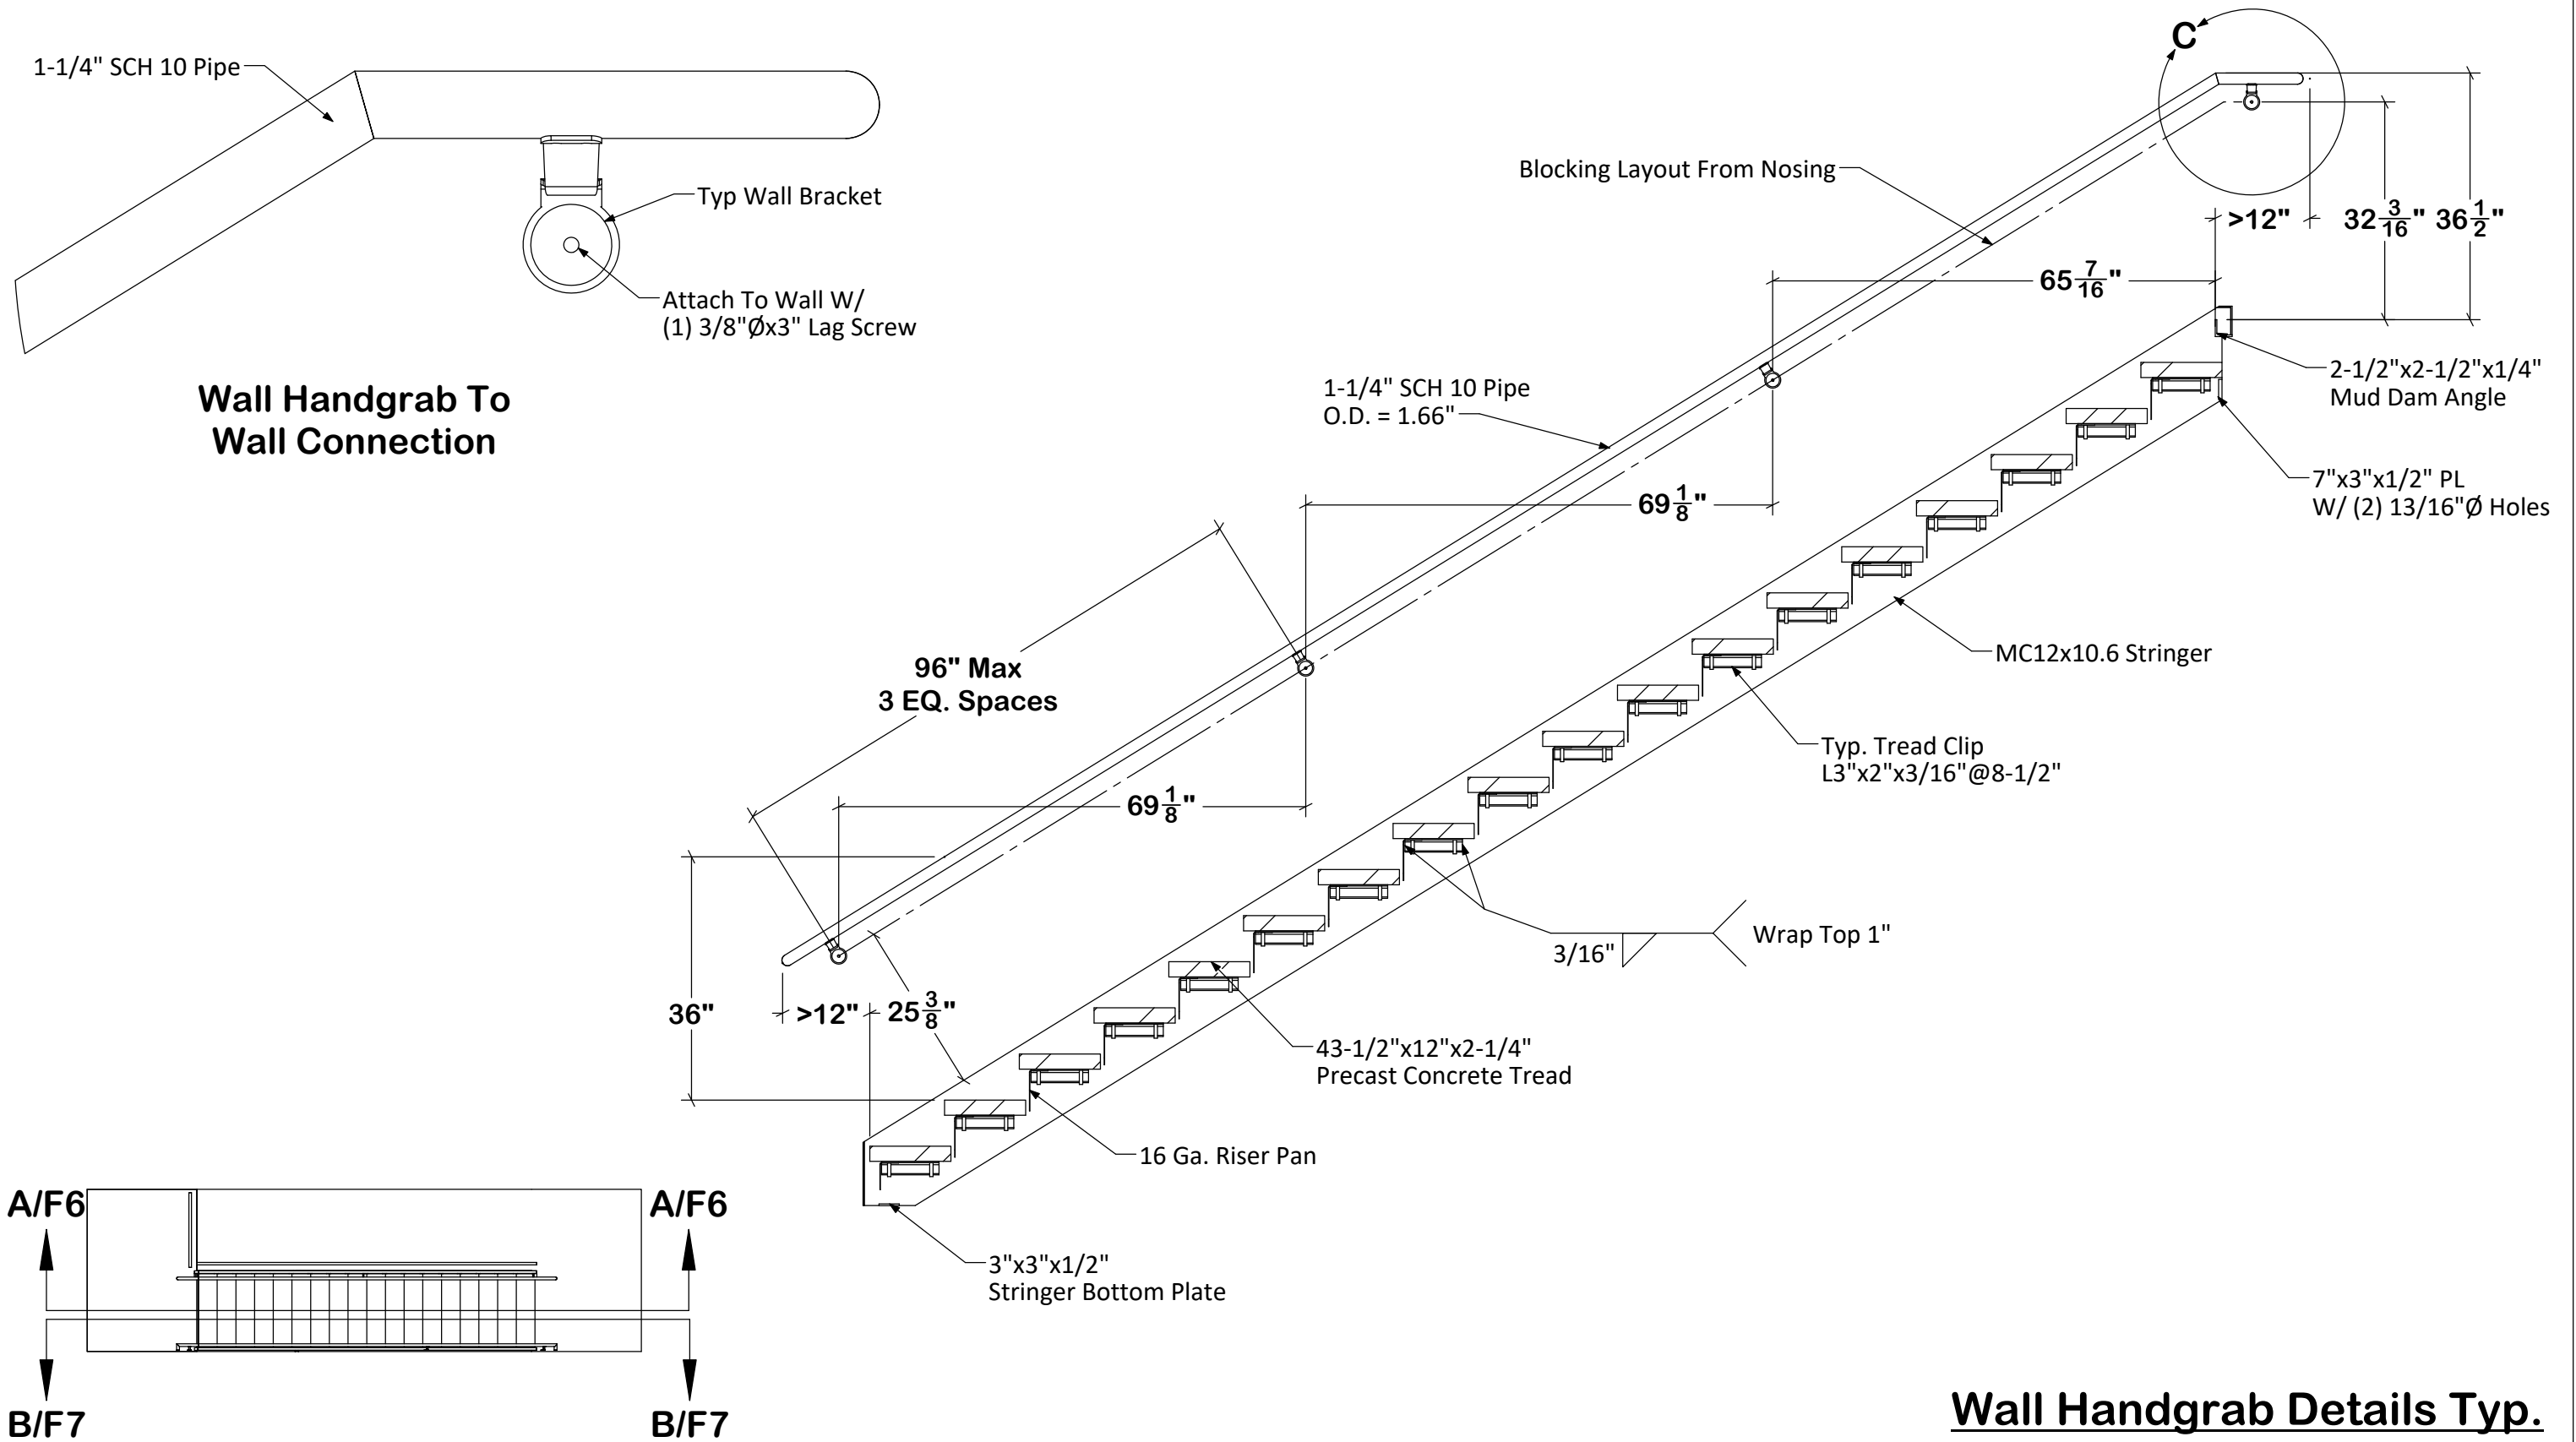

Index	Date	Description	By



Mile High Metal Works, Inc.
7399 Miller Court, Unit A, Frederick, CO 80504
Office 303-485-8283 Fax 303-485-8206

Project Name:
CSI Construction - Flats At
Sand Creek

Description:
Bld 3W Stair Core

Date:
6/5/2026

Job #:
590-674




Color:
Red Oxide
Primed

By:
DCR

Rev:
0

Drawing:
F20

T:\590 Flats at Sand Creek (CO Springs)\Solidworks\Stairs\Bld 3W Stair Core FAB

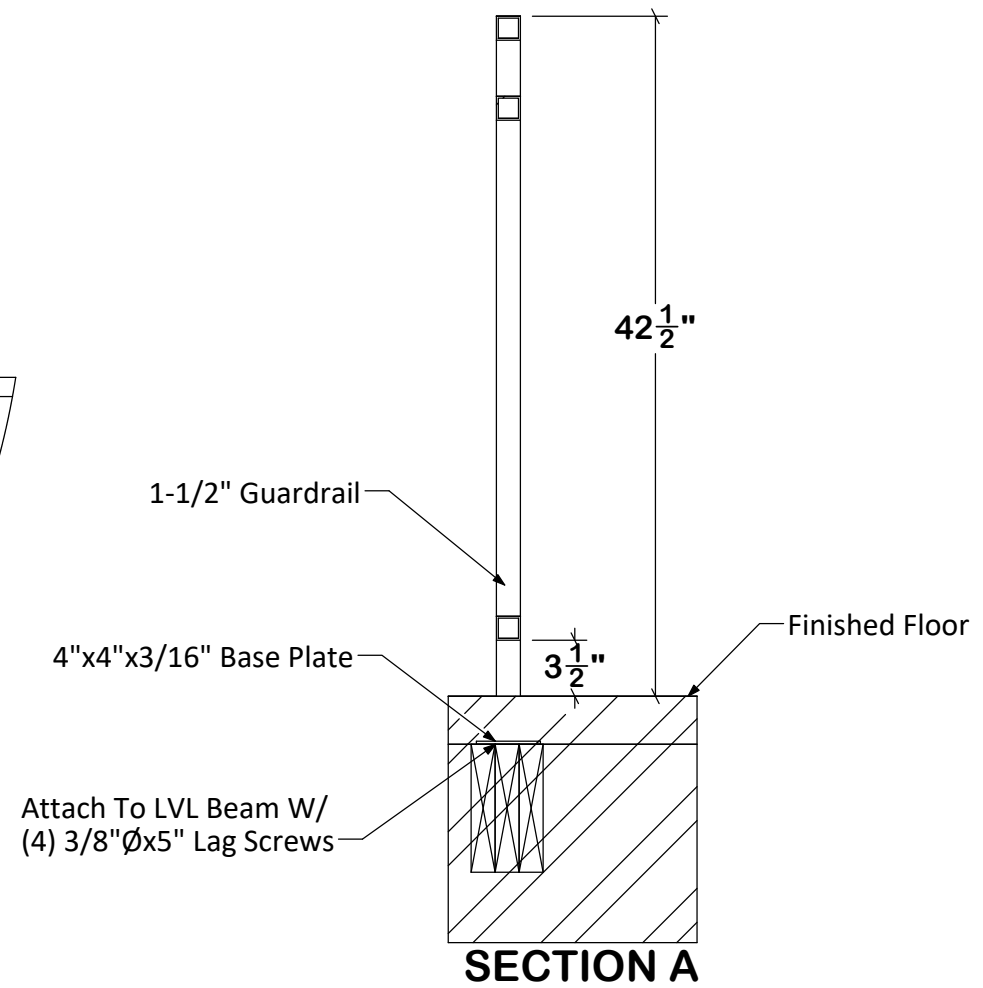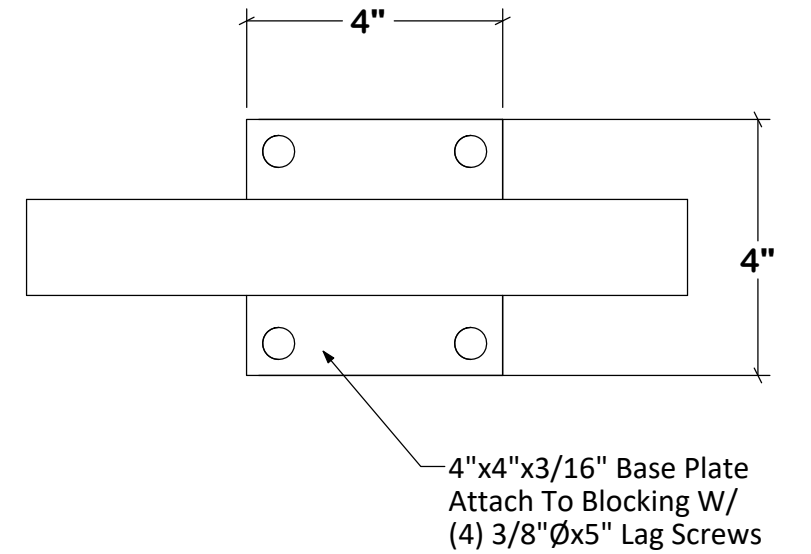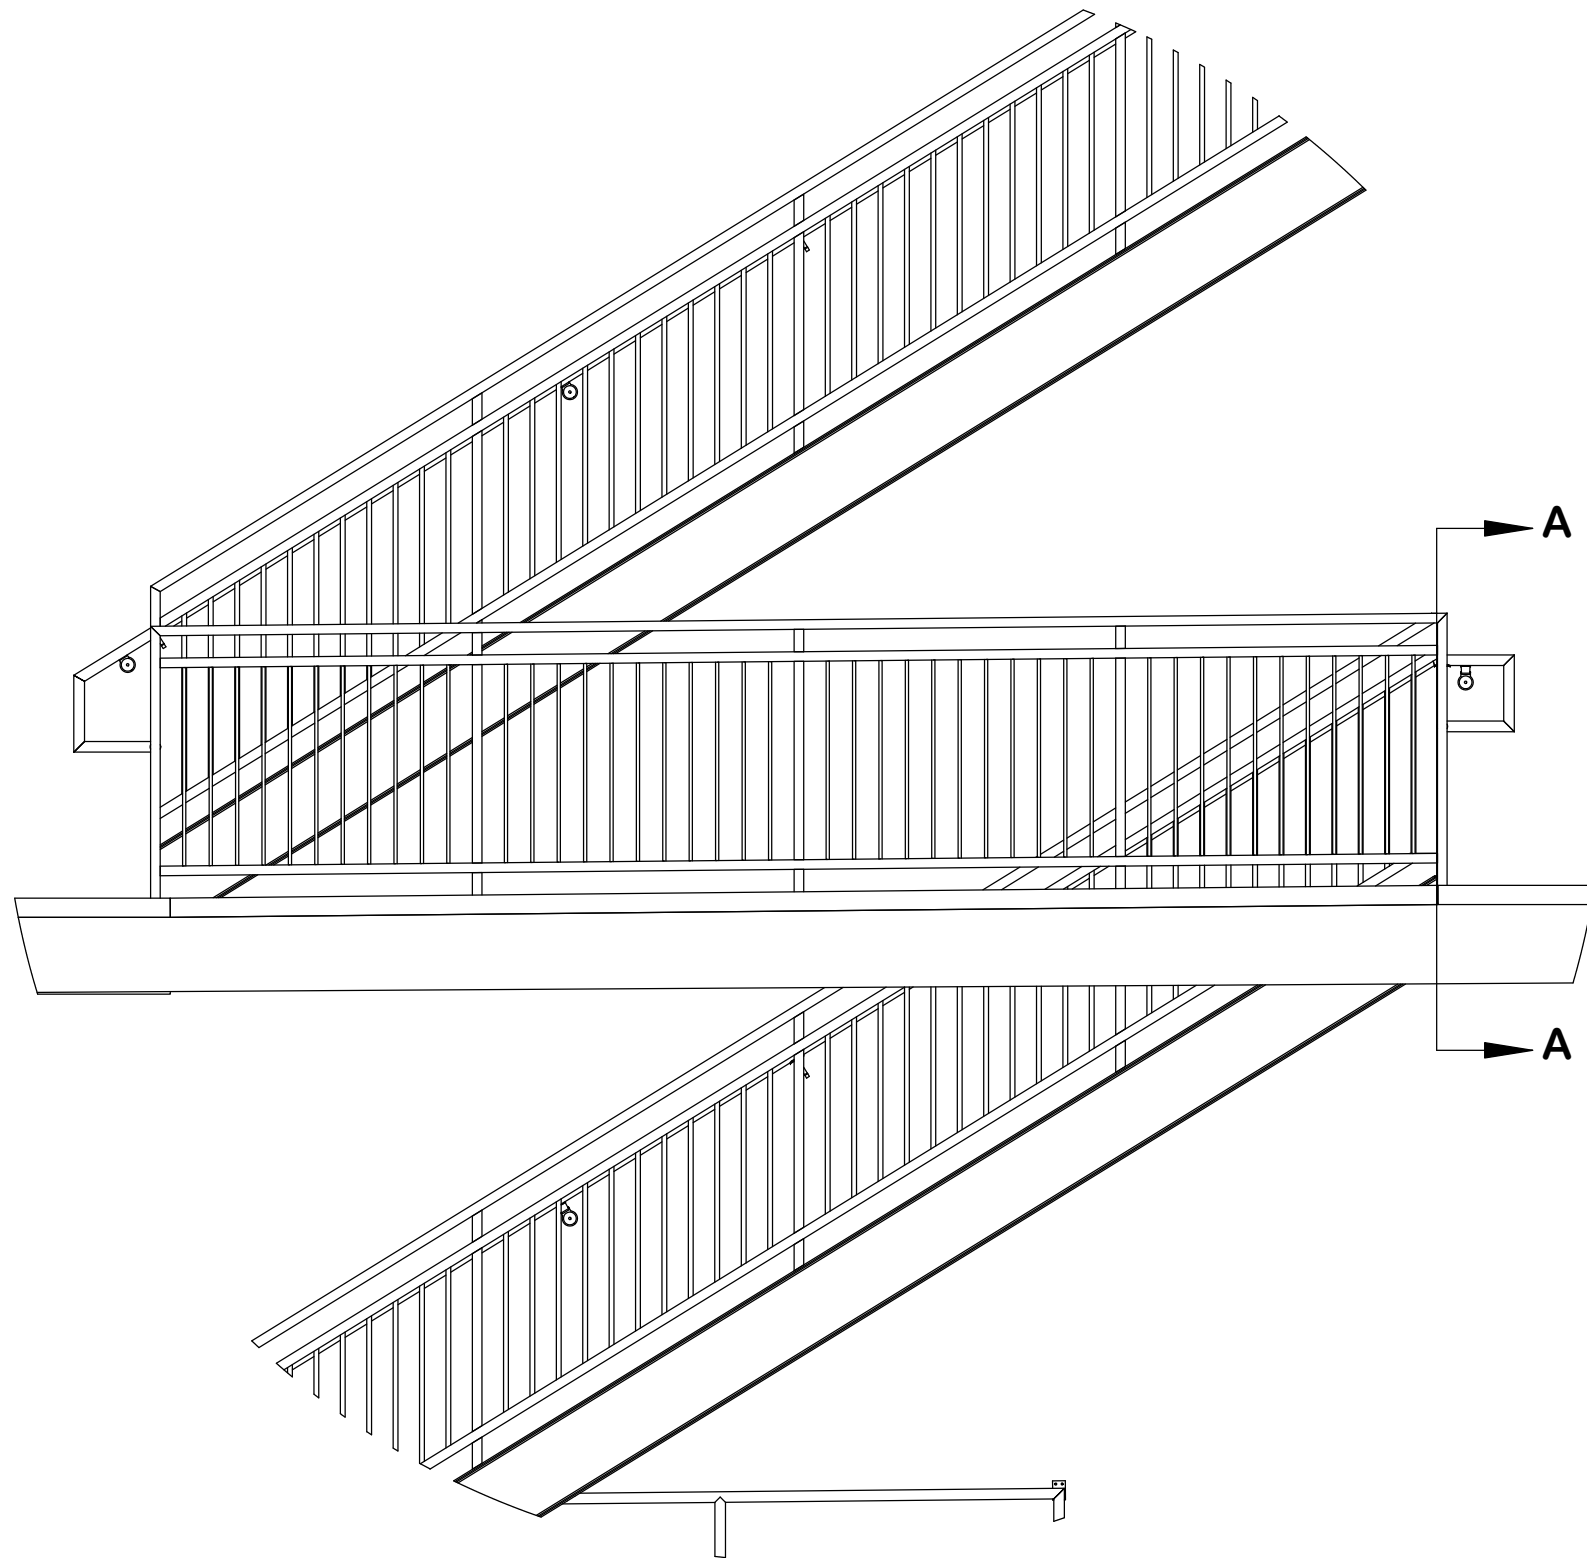

Landing Guardrail Details

Index	Date	Description	By


Mile High Metal Works, Inc.
7399 Miller Court, Unit A, Frederick, CO 80504
Office 303-485-8283 Fax 303-485-8206

Project Name:
CSI Construction - Flats At
Sand Creek

Description:
Bld 3W Stair Core


Date:
6/5/2026
Job #:
590-674

Color:
Red Oxide
Primed


By:
DCR
Rev:
0

Drawing:
F21

T:\590 Flats at Sand Creek (CO Springs)\Solidworks\Stairs\Bld 3W Stair Core FAB

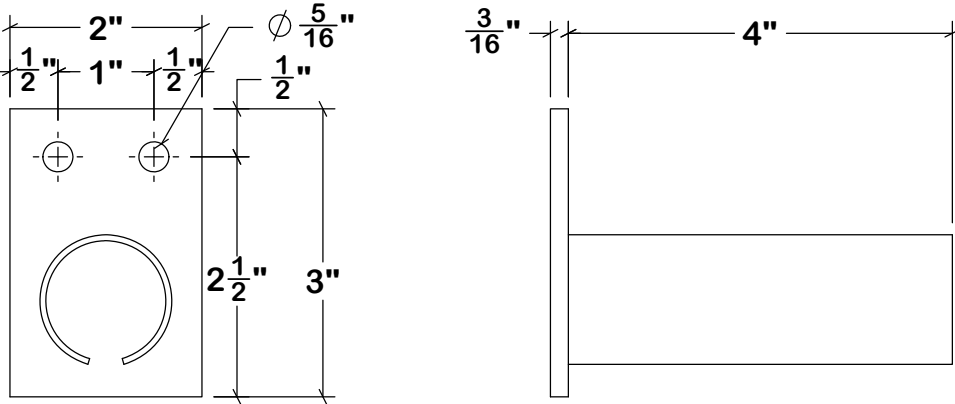

Pipe Sleeve Details

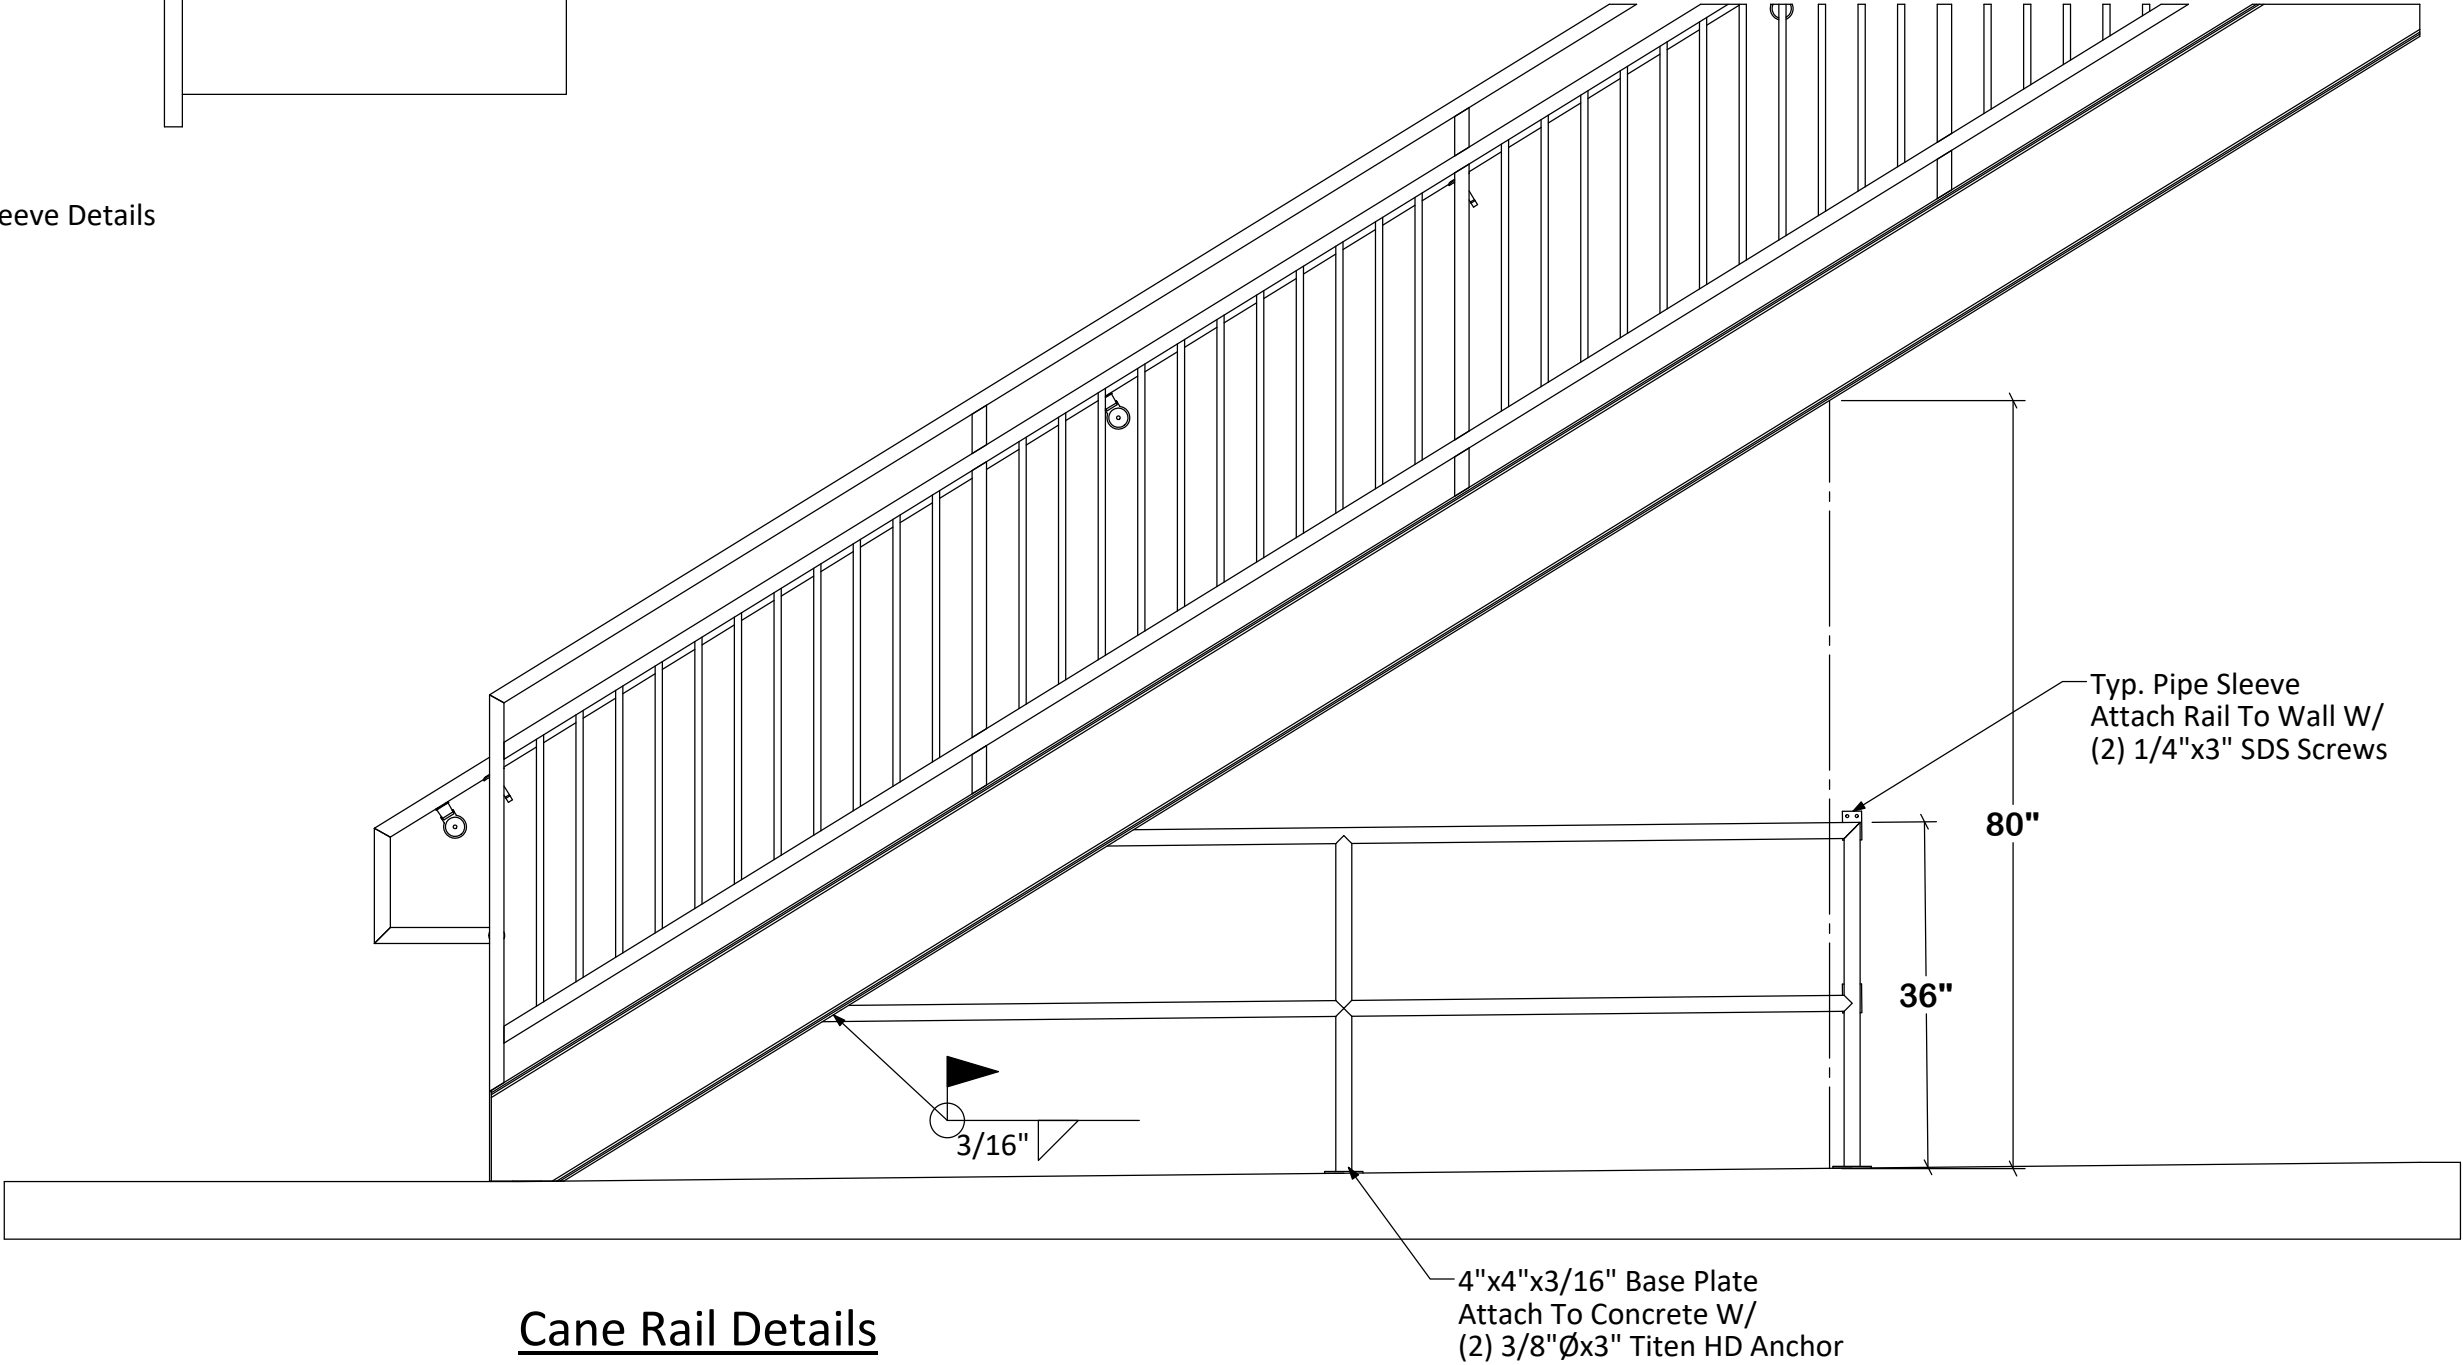

Cane Rail Details

Index	Date	Description	By



Mile High Metal Works, Inc.
7399 Miller Court, Unit A, Frederick, CO 80504
Office 303-485-8283 Fax 303-485-8206

Project Name:
CSI Construction - Flats At
Sand Creek

Description:
Bld 3W Stair Core

Date:
6/5/2026

Job #:
590-674


Color:
Red Oxide
Primed

By:
DCR

Rev:
0

Drawing:
F22

T:\590 Flats at Sand Creek (CO Springs)\Solidworks\Stairs\Bld 3W Stair Core FAB

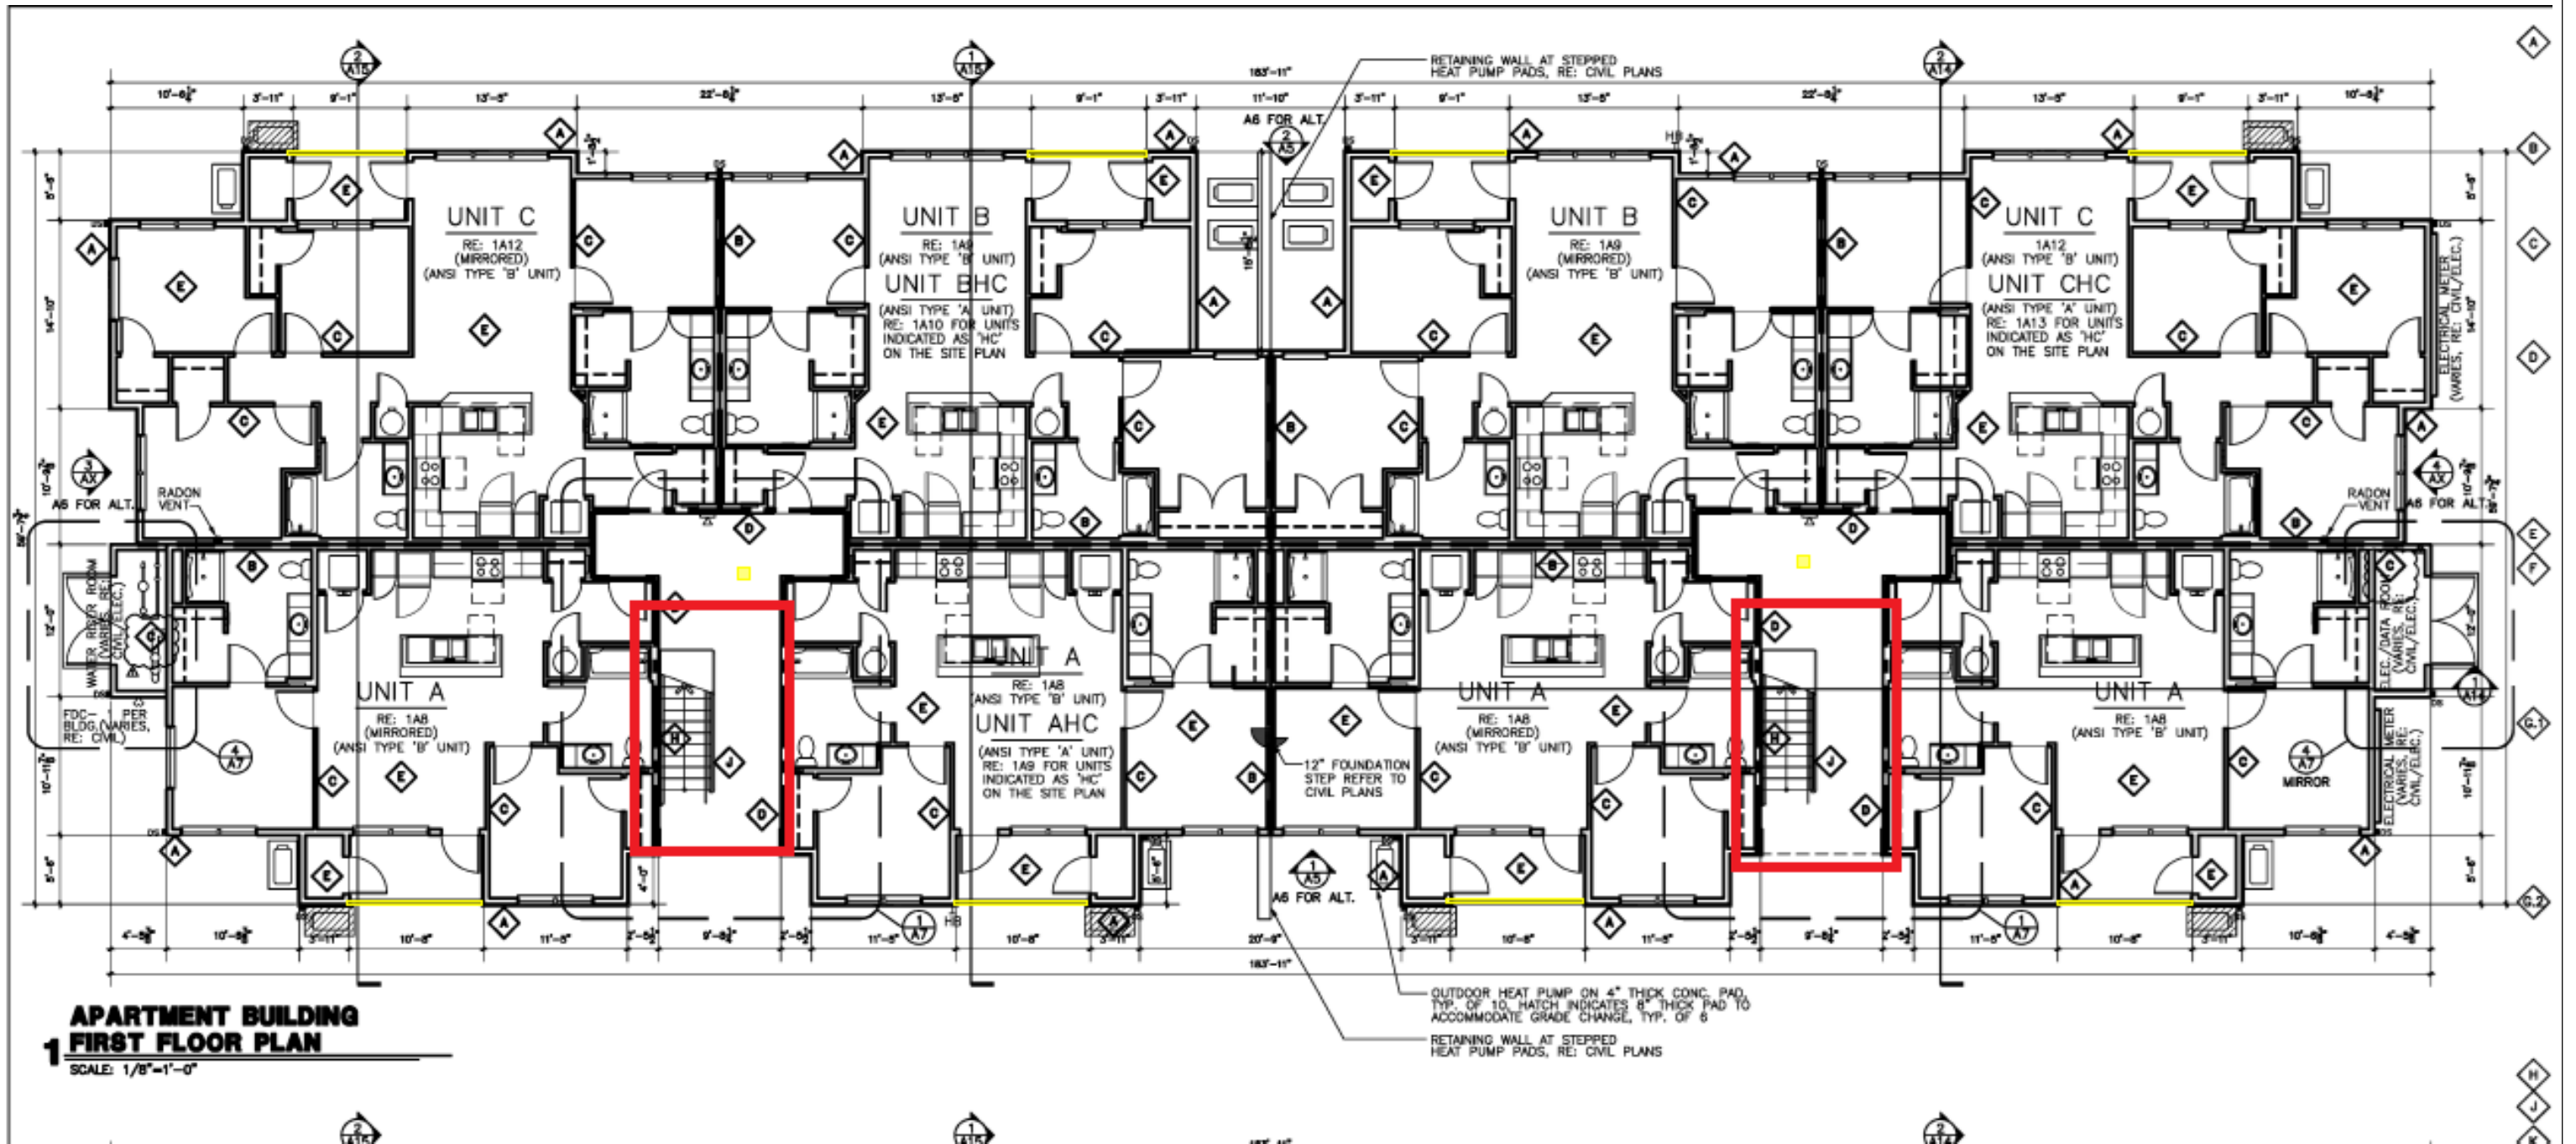

Index	Date	Description	By



Mile High Metal Works, Inc.
7399 Miller Court, Unit A, Frederick, CO 80504
Office 303-485-8283 Fax 303-485-8206

Project Name:
CSI Construction - Flats At
Sand Creek

Description:
Bld 3W Stair Core

Date:
6/5/2026

Job #:
590-674

Color:
Red Oxide
Primed

By:
DCR

Rev:
0

Drawing:
F23